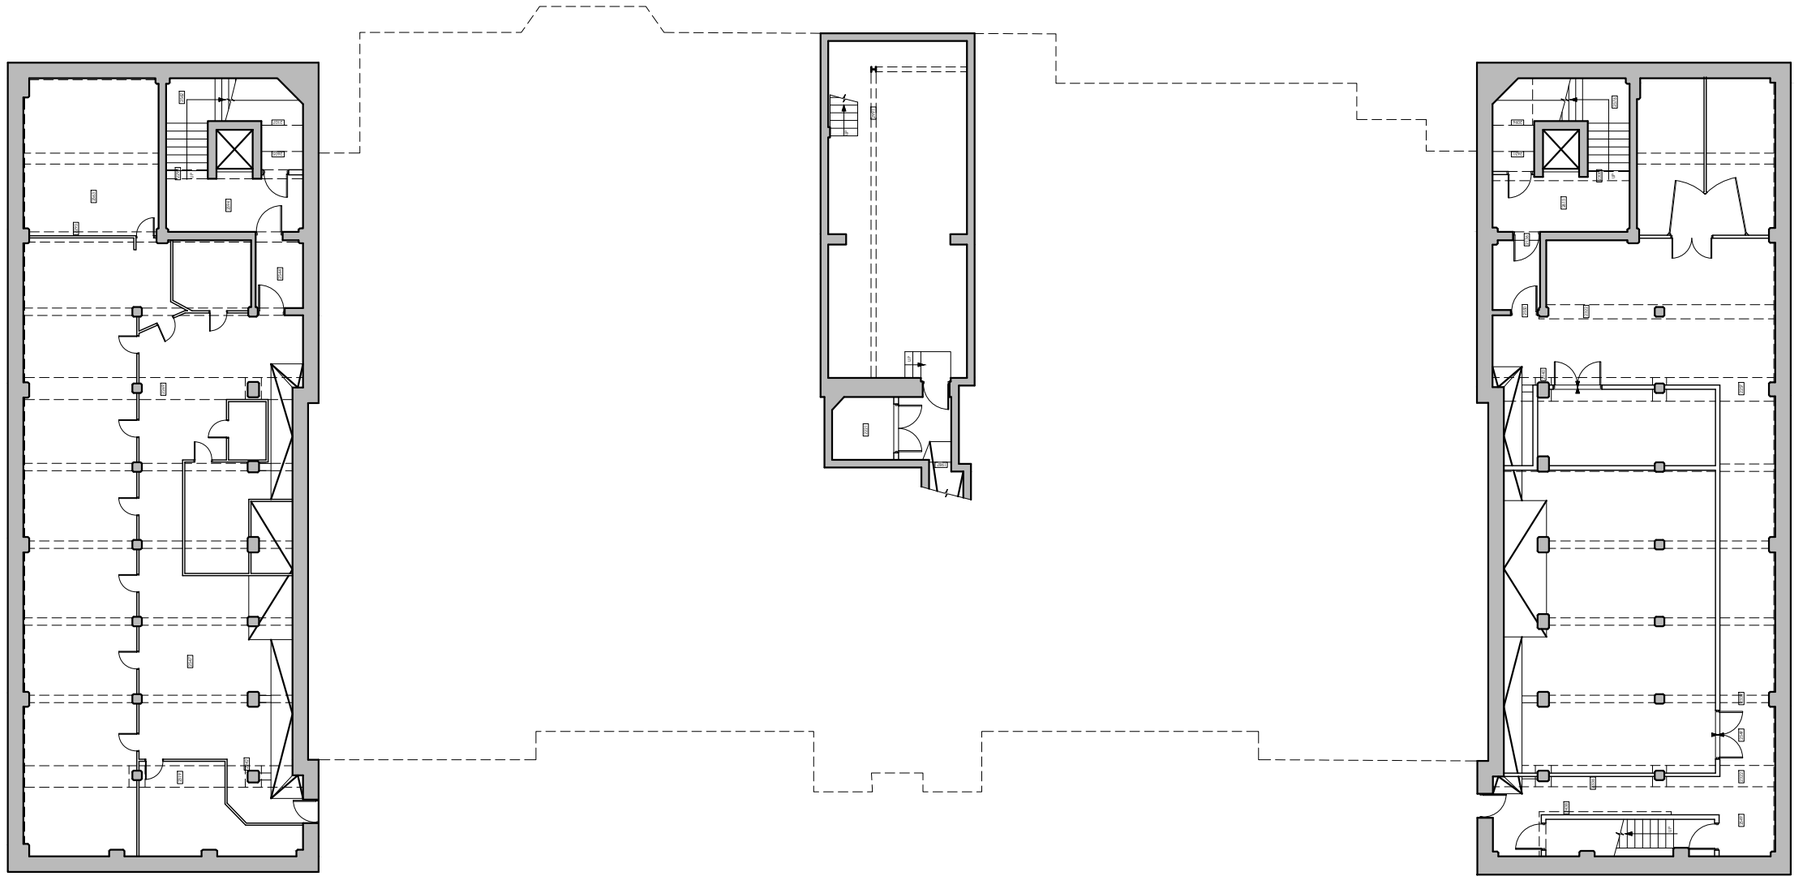


Existing Basement Floor Plan
Scale 1:200 @ A3

0 10m

Issued For
PLANNING

General Notes:

THIS DRAWING HAS BEEN PREPARED BY MICHAEL EALES ARCHITECTS AND THE DATA CONTAINED HEREIN MAY BE USED OR REPRODUCED ONLY WITH MICHAEL EALES ARCHITECTS' APPROVAL.

Rev.	Description	Date	Signed	Checked


A3 Scale	Date	Drawn by	Checked by
1:200@A3	03.08.26	RT	ME

Drawing Title
Existing Basement Floor Plan

Project
The Grange, Bank Ln, London
SW15 5JT

ME ARCHITECTS
UNIT 201 Media House,
Sopers Road, Potters Bar EN6 4RY
T - 07764 496 345
E - info@me-architects.co.uk

Project no.	Drawing no.	Revision
26/393	101	00

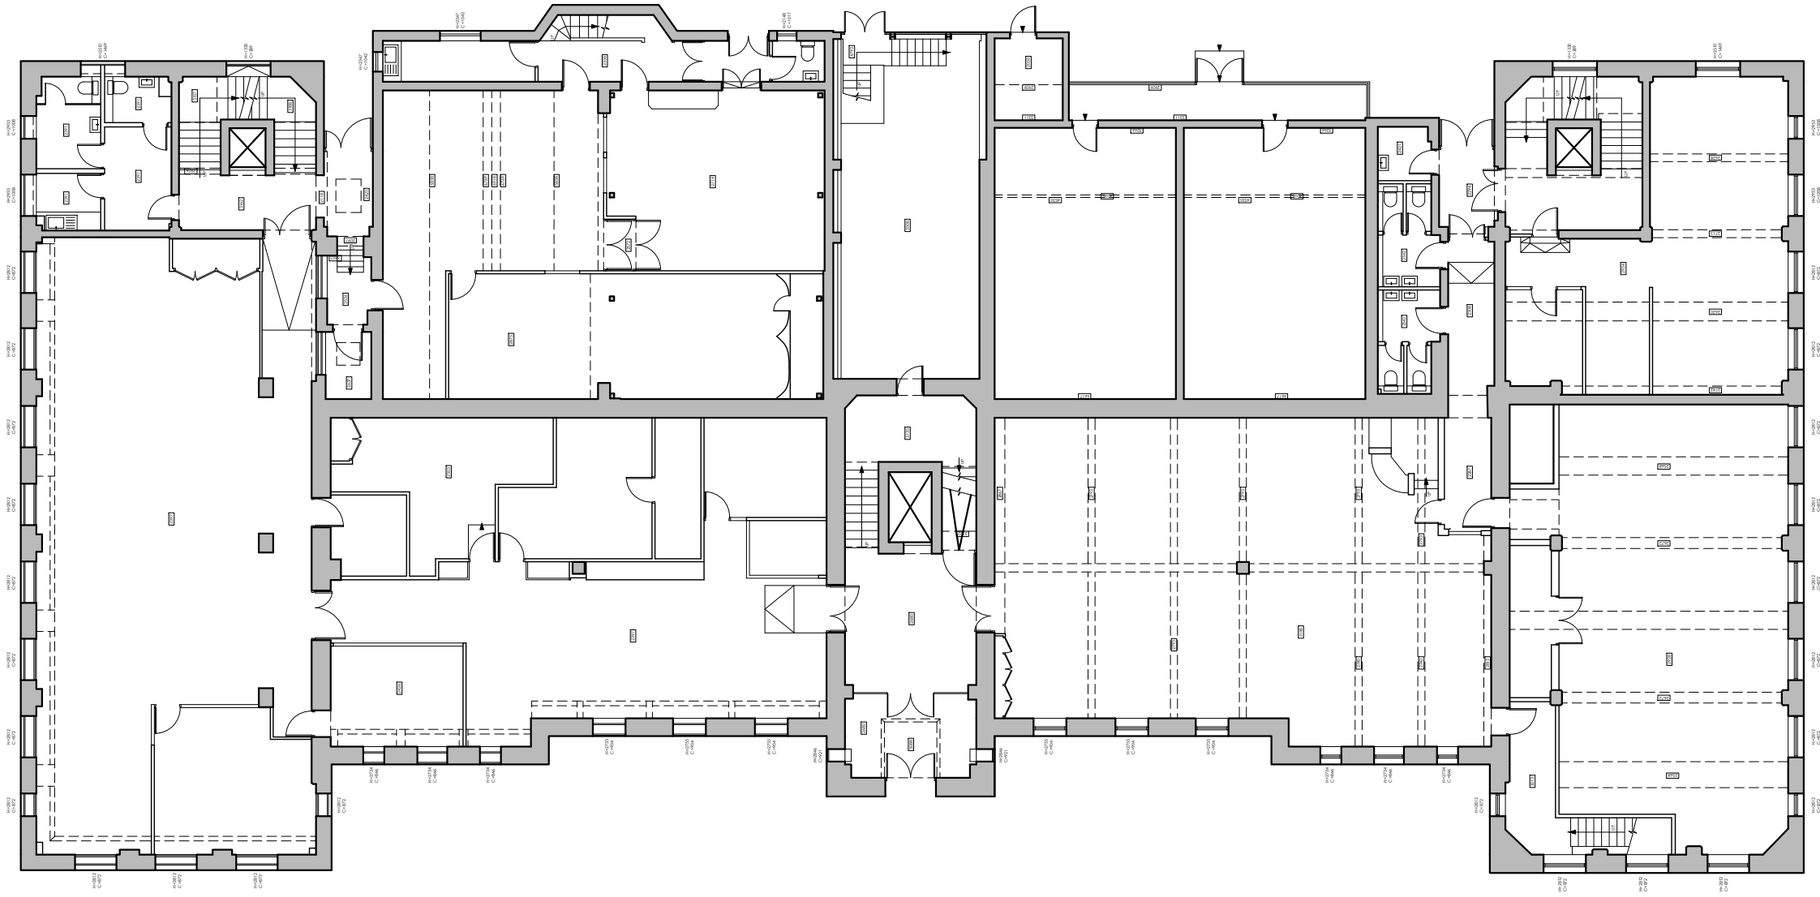

Existing Ground Floor Plan
Scale 1:200 @ A3

0 10m

Issued For
PLANNING

General Notes:

THIS DRAWING HAS BEEN PREPARED BY MICHAEL EALES ARCHITECTS AND THE DATA CONTAINED HEREIN MAY BE USED OR REPRODUCED ONLY WITH MICHAEL EALES ARCHITECTS' APPROVAL.

Rev.	Description	Date	Signed	Checked


A3 Scale	Date	Drawn by	Checked by
1:200@A3	03.08.26	RT	ME

Drawing Title
Existing Ground Floor Plan

Project
The Grange, Bank Ln, London SW15 5JT

ME ARCHITECTS
UNIT 201 Media House,
Sopers Road, Potters Bar EN6 4RY
T - 07764 496 345
E - info@me-architects.co.uk

Project no.	Drawing no.	Revision
26/393	102	00

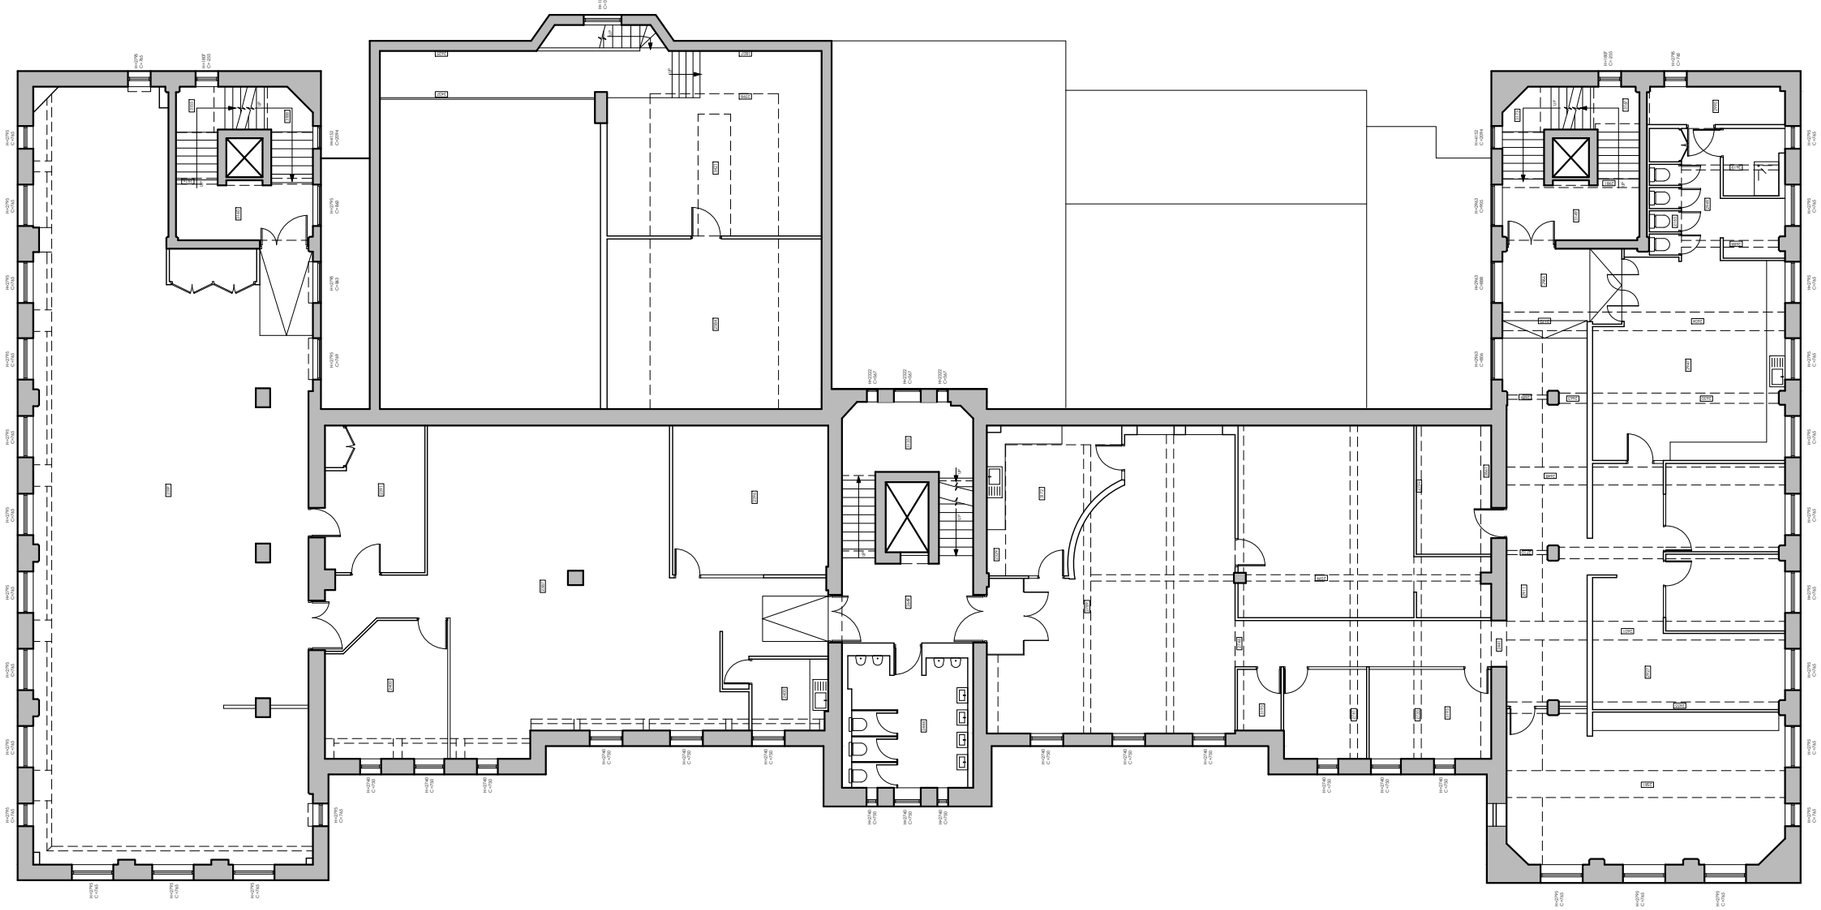

Existing First Floor Plan
Scale 1:200 @ A3

0 10m

Issued For
PLANNING

General Notes:

THIS DRAWING HAS BEEN PREPARED BY MICHAEL EALES ARCHITECTS AND THE DATA CONTAINED HEREIN MAY BE USED OR REPRODUCED ONLY WITH MICHAEL EALES ARCHITECTS' APPROVAL.

Rev.	Description	Date	Signed	Checked


A3 Scale	Date	Drawn by	Checked by
1:200@A3	03.08.26	RT	ME

Drawing Title
Existing First Floor Plan

Project
The Grange, Bank Ln, London
SW15 5JT

ME ARCHITECTS
UNIT 201 Media House,
Sopers Road, Potters Bar EN6 4RY
T - 07764 496 345
E - info@me-architects.co.uk

Project no.	Drawing no.	Revision
26/393	103	00

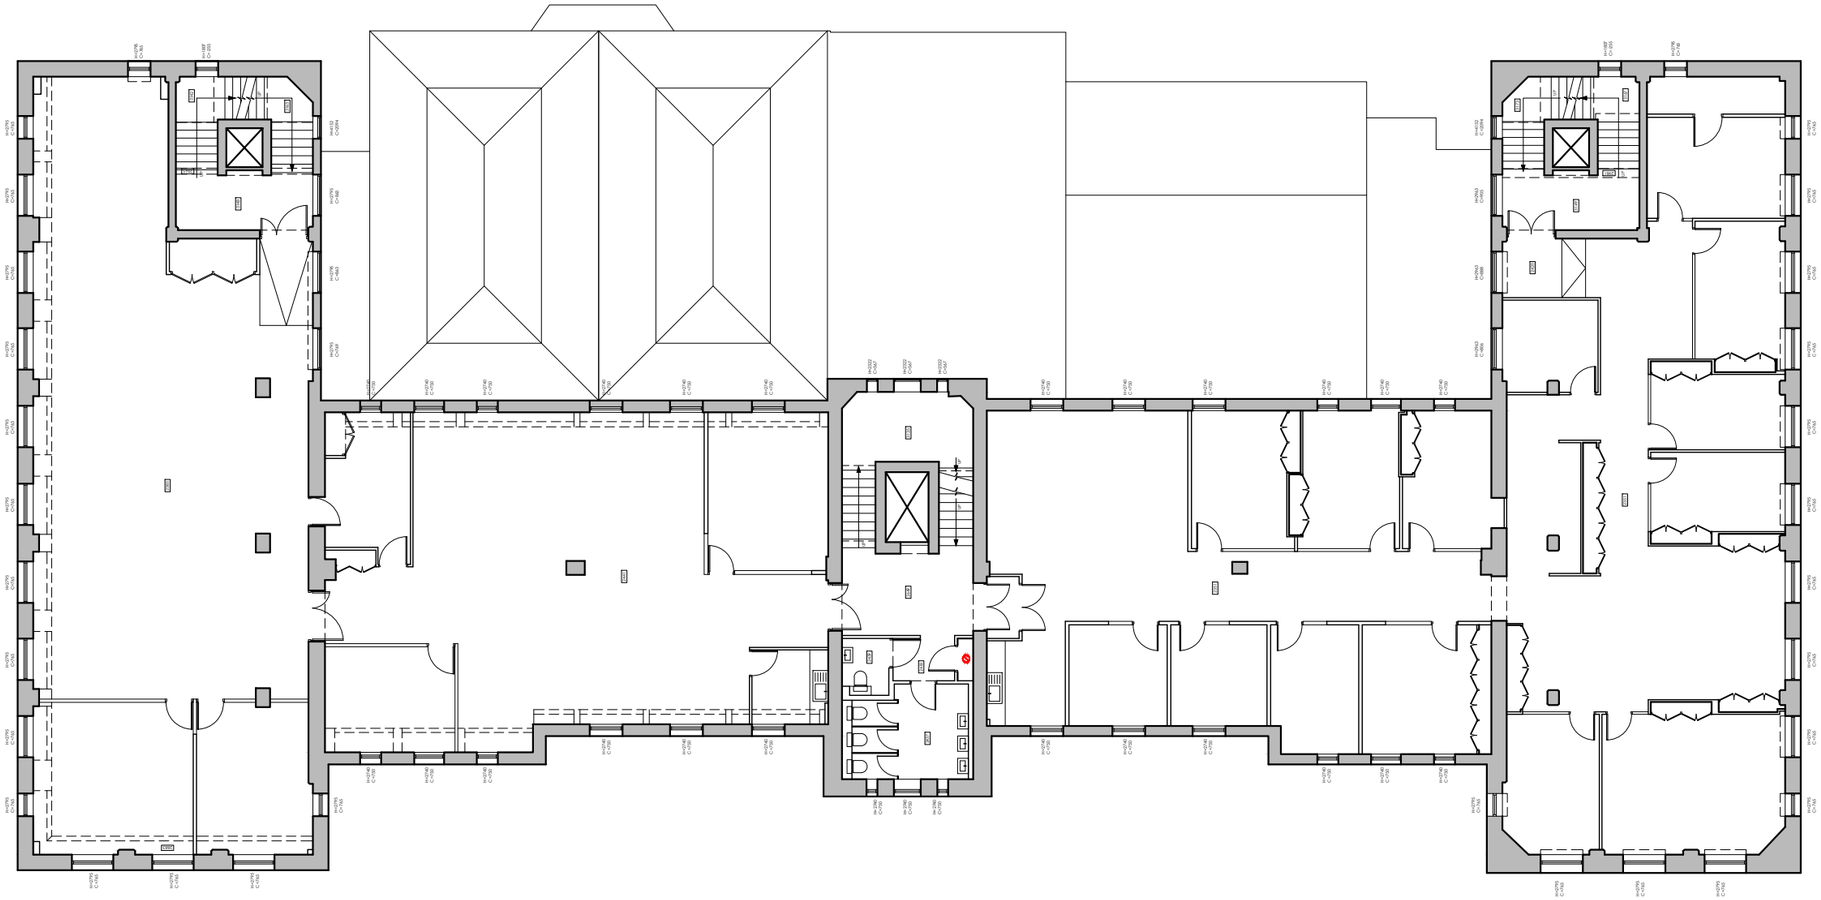

Existing Second Floor Plan
Scale 1:200 @ A3

0 10m

Issued For
PLANNING

General Notes:

THIS DRAWING HAS BEEN PREPARED BY MICHAEL EALES ARCHITECTS AND THE DATA CONTAINED HEREIN MAY BE USED OR REPRODUCED ONLY WITH MICHAEL EALES ARCHITECTS' APPROVAL.

Rev.	Description	Date	Signed	Checked


A3 Scale	Date	Drawn by	Checked by
1:200@A3	03.08.26	RT	ME

Drawing Title
Existing Second Floor Plan

Project
The Grange, Bank Ln, London SW15 5JT

ME ARCHITECTS
UNIT 201 Media House,
Sopers Road, Potters Bar EN6 4RY
T - 07764 496 345
E - info@me-architects.co.uk

Project no.	Drawing no.	Revision
26/393	104	00

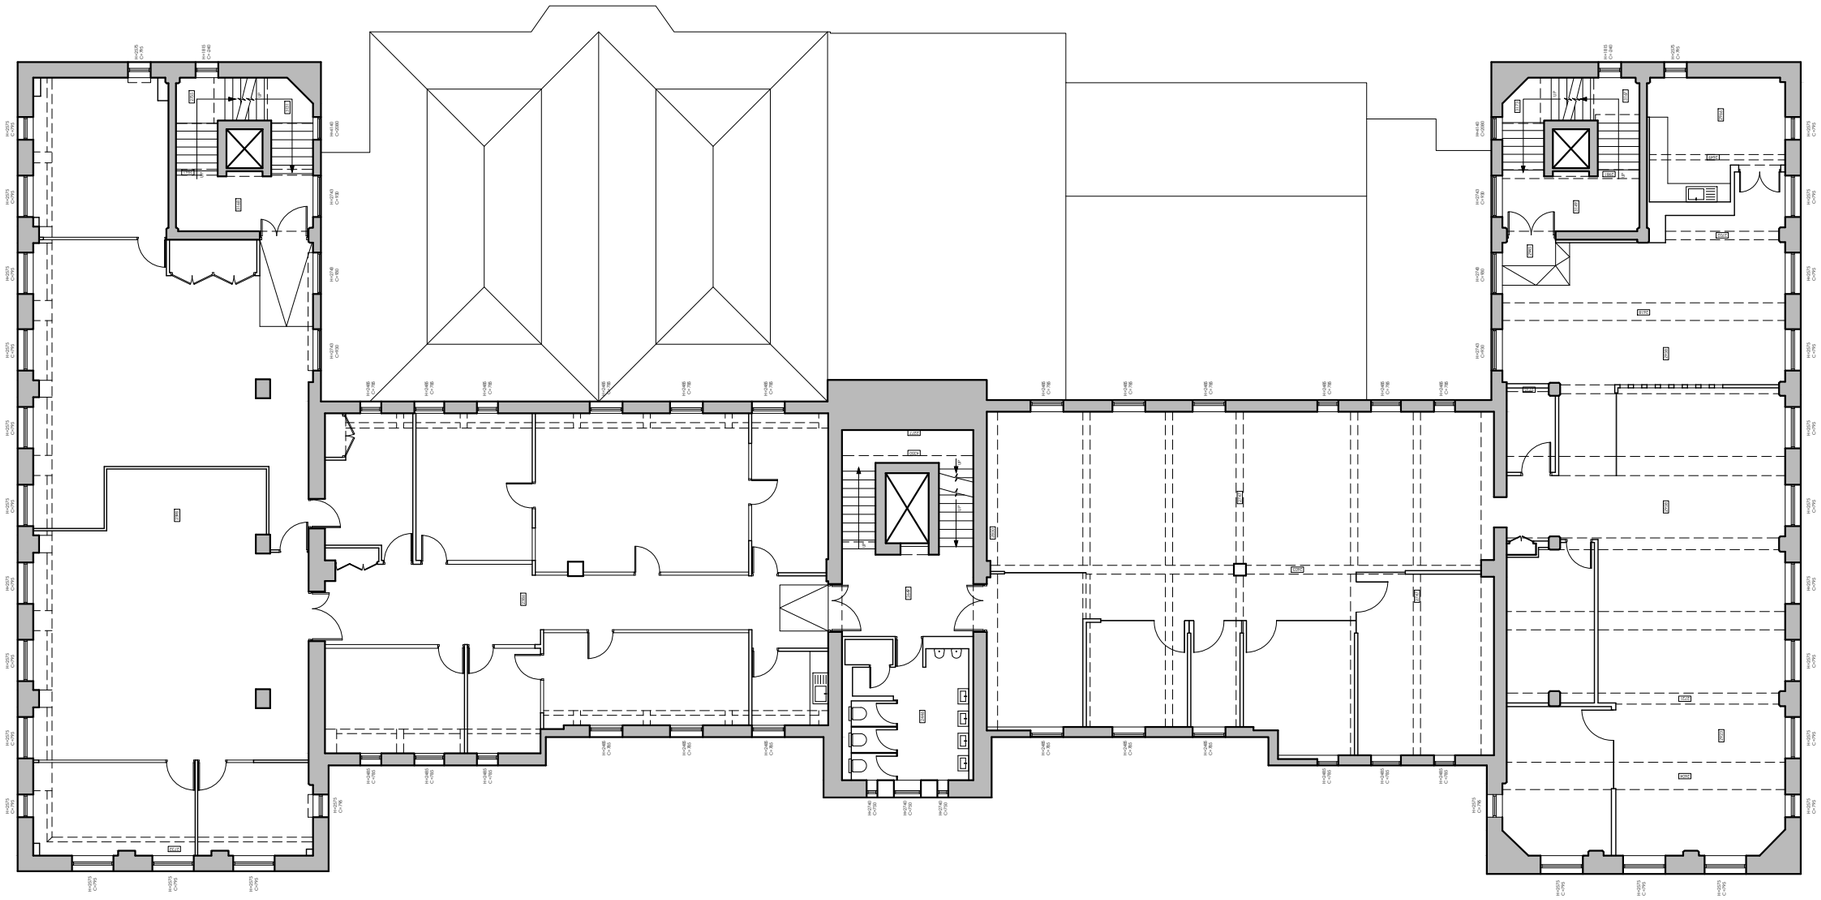

Existing Third Floor Plan
Scale 1:200 @ A3

0 10m

Issued For
PLANNING

General Notes:
THIS DRAWING HAS BEEN PREPARED BY MICHAEL EALES ARCHITECTS AND THE DATA CONTAINED HEREIN MAY BE USED OR REPRODUCED ONLY WITH MICHAEL EALES ARCHITECTS' APPROVAL.

Rev.	Description	Date	Signed	Checked


A3 Scale	Date	Drawn by	Checked by
1:200@A3	03.08.26	RT	ME

Drawing Title
Existing Third Floor Plan

Project
The Grange, Bank Ln, London SW15 5JT

ME ARCHITECTS
UNIT 201 Media House,
Sopers Road, Potters Bar EN6 4RY
T - 07764 496 345
E - info@me-architects.co.uk

Project no.	Drawing no.	Revision
26/393	105	00

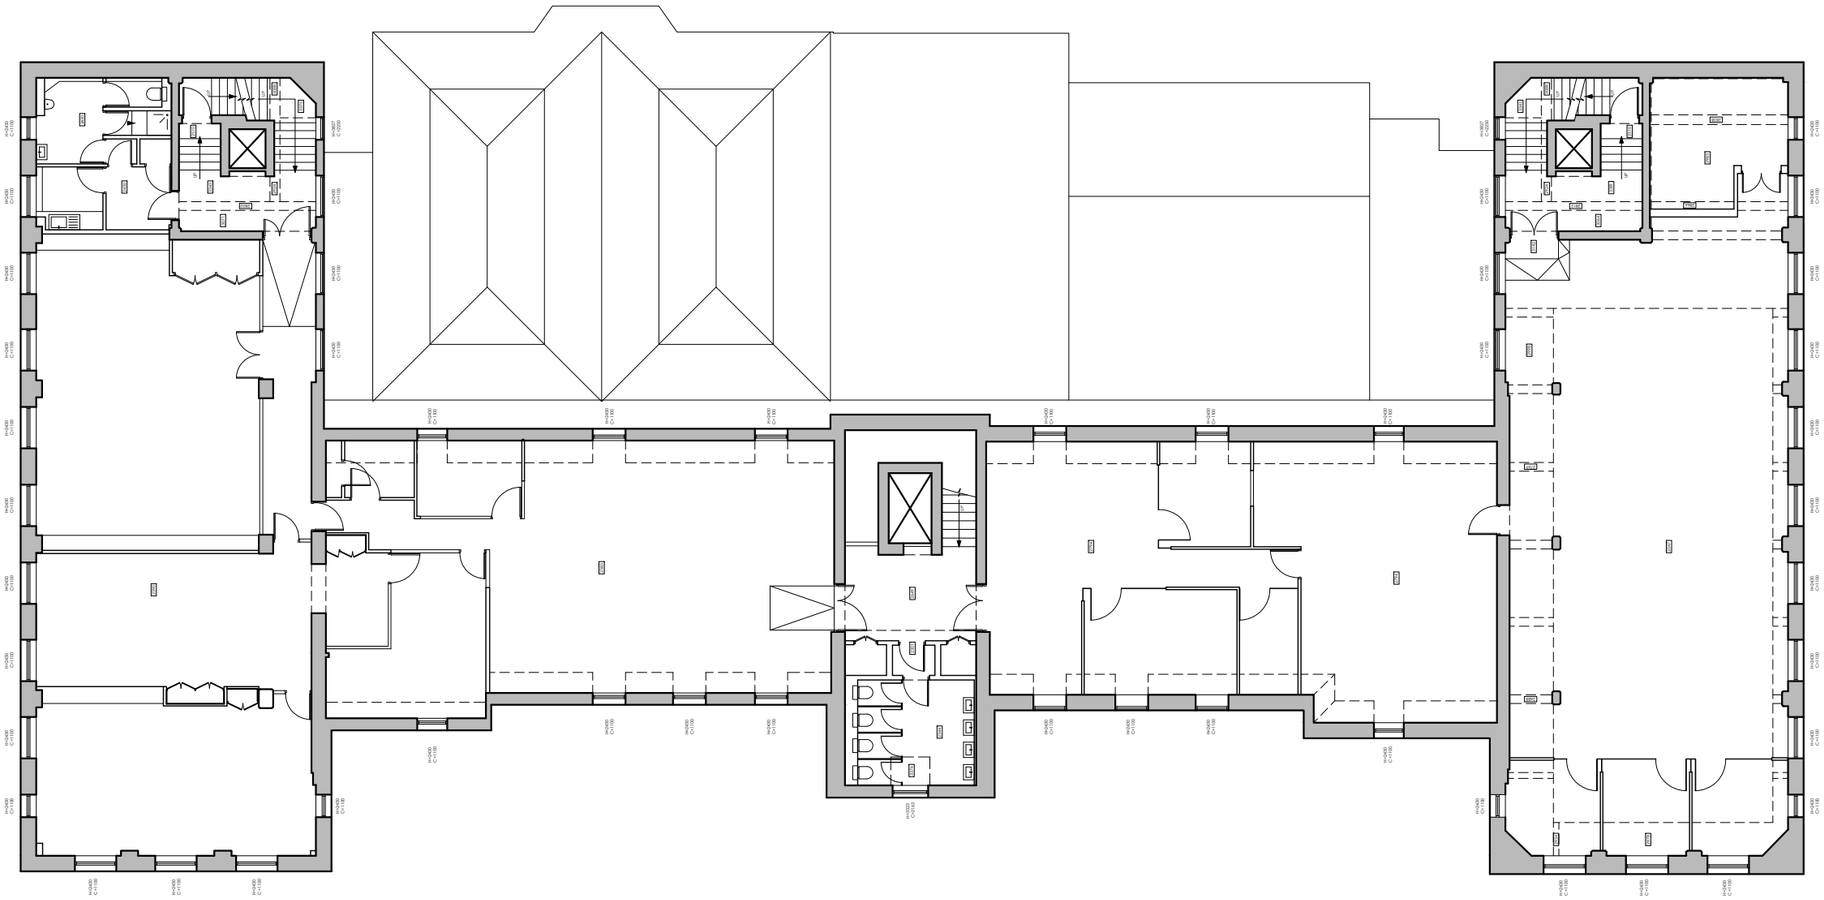

Existing Fourth Floor Plan
Scale 1:200 @ A3

0 10m

Issued For
PLANNING

General Notes:

THIS DRAWING HAS BEEN PREPARED BY MICHAEL EALES ARCHITECTS AND THE DATA CONTAINED HEREIN MAY BE USED OR REPRODUCED ONLY WITH MICHAEL EALES ARCHITECTS' APPROVAL.

Rev.	Description	Date	Signed	Checked


A3 Scale	Date	Drawn by	Checked by
1:200@A3	03.08.26	RT	ME

Drawing Title
Existing Fourth Floor Plan

Project
The Grange, Bank Ln, London
SW15 5JT

ME ARCHITECTS
UNIT 201 Media House,
Sopers Road, Potters Bar EN6 4RY
T - 07764 496 345
E - info@me-architects.co.uk

Project no.	Drawing no.	Revision
26/393	106	00

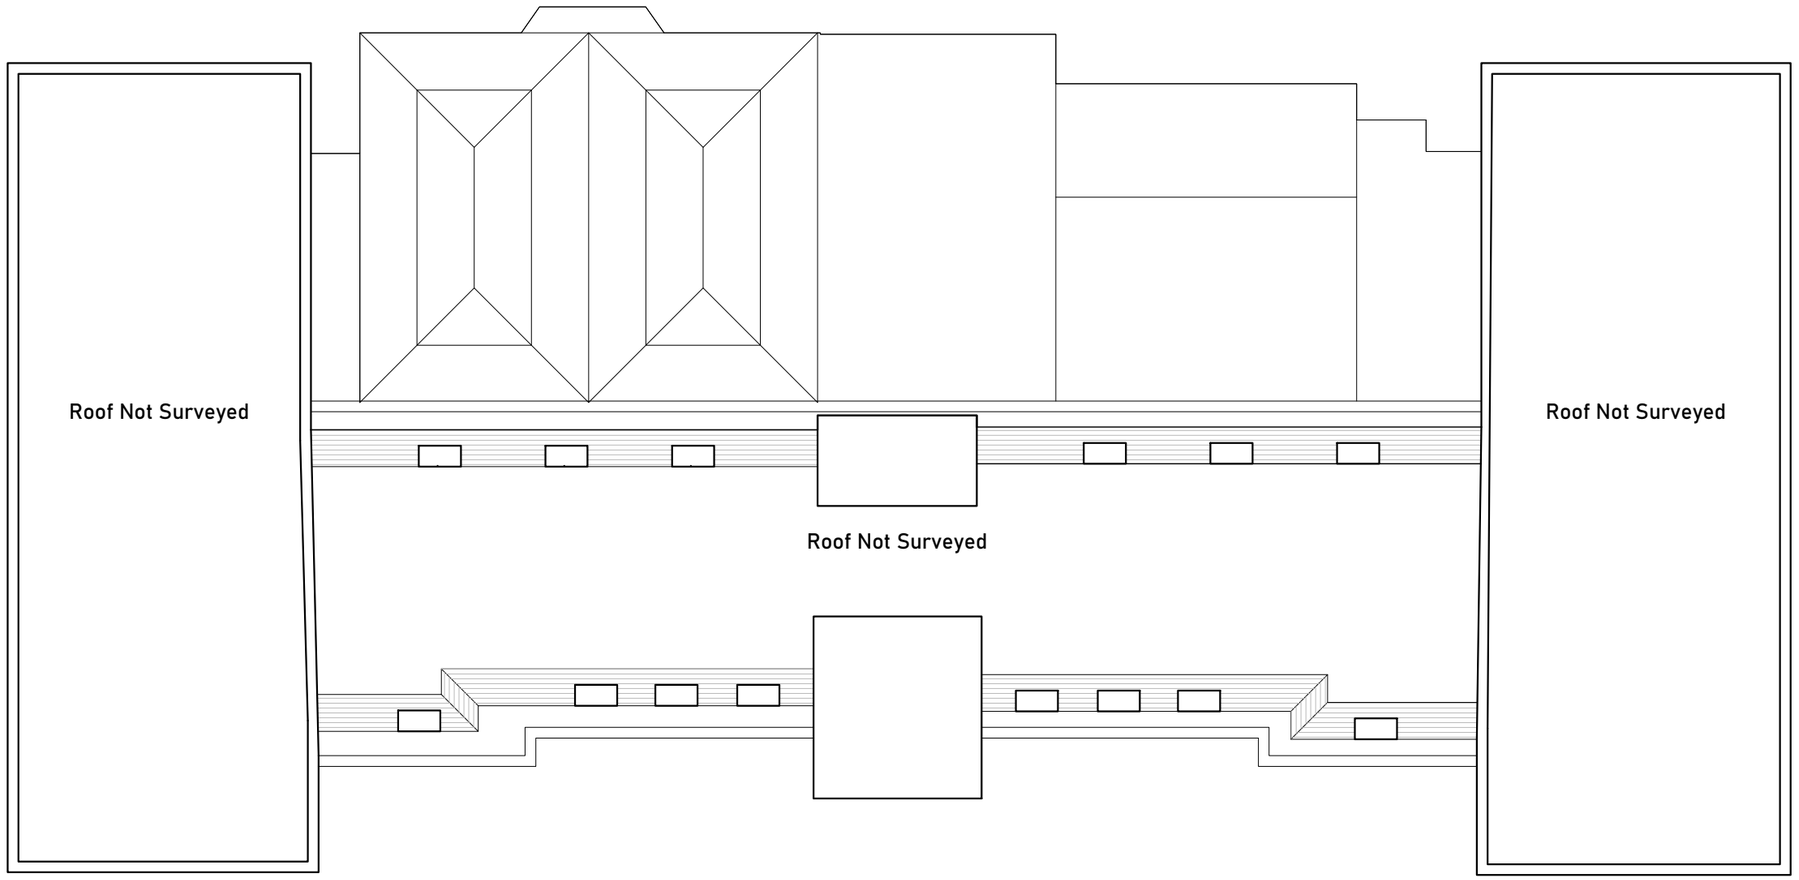

Existing Roof Plan
Scale 1:200 @ A3

0 10m

Issued For
PLANNING

General Notes:

THIS DRAWING HAS BEEN PREPARED BY MICHAEL EALES ARCHITECTS AND THE DATA CONTAINED HEREIN MAY BE USED OR REPRODUCED ONLY WITH MICHAEL EALES ARCHITECTS' APPROVAL.

Rev.	Description	Date	Signed	Checked

A3 Scale	Date	Drawn by	Checked by
1:200@A3	03.08.26	RT	ME

Drawing Title
Existing Roof Plan

Project
The Grange, Bank Ln, London
SW15 5JT

ME ARCHITECTS
UNIT 201 Media House,
Sopers Road, Potters Bar EN6 4RY
T - 07764 496 345
E - info@me-architects.co.uk

Project no.	Drawing no.	Revision
26/393	107	00