
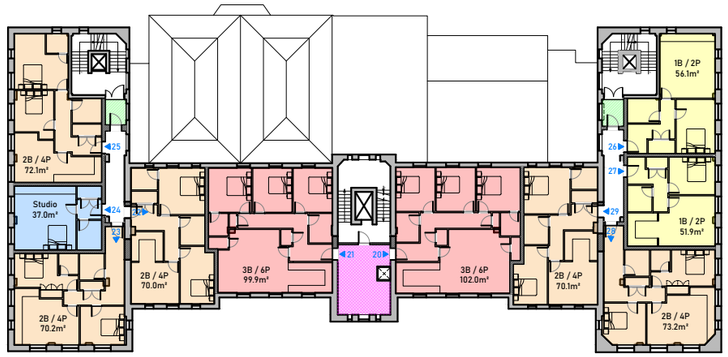



Proposed Second Floor Plan

Scale 1:500 @ A3

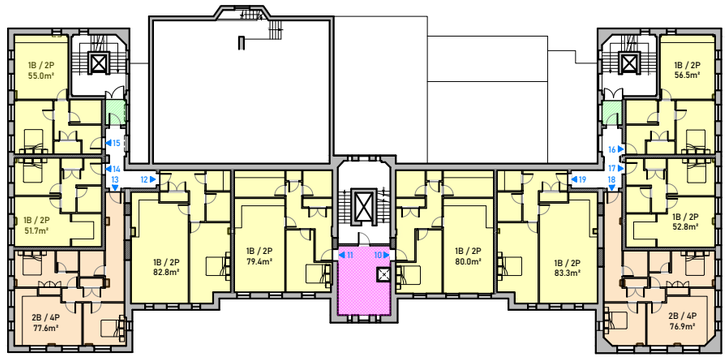


Proposed First Floor Plan

Scale 1:500 @ A3

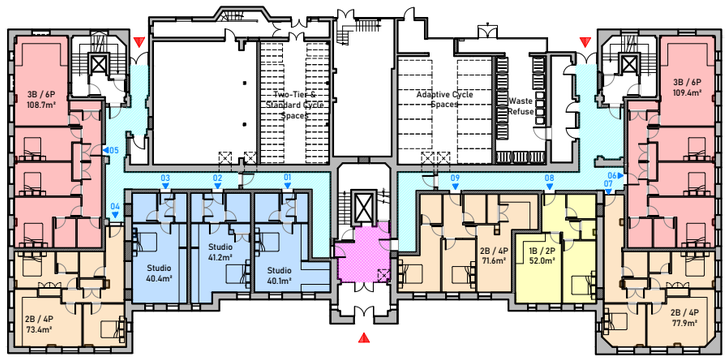


Proposed Ground Floor Plan

Scale 1:500 @ A3

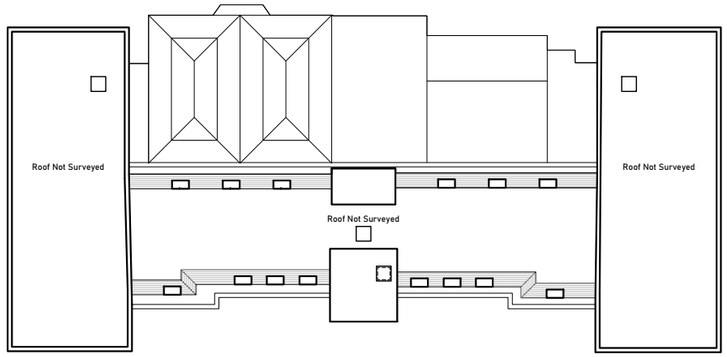


Proposed Roof Plan

Scale 1:500 @ A3

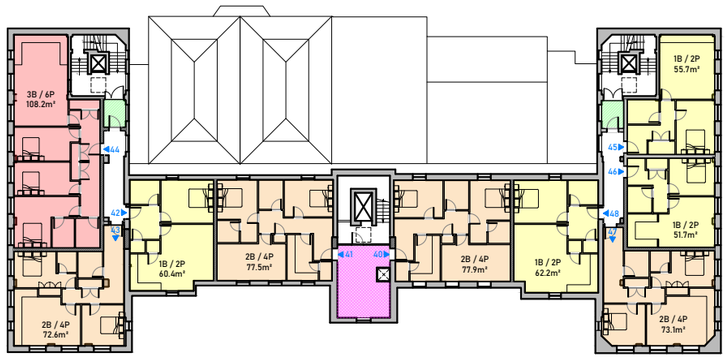

Proposed Fourth Floor Plan

Scale 1:500 @ A3

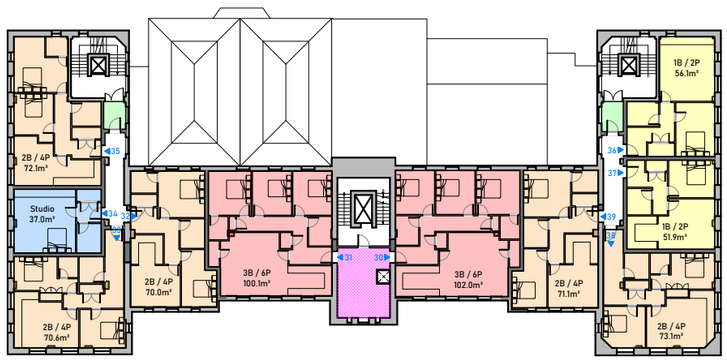

Proposed Third Floor Plan

Scale 1:500 @ A3

LEGEND:

- Studio Unit
- 1 Bed / 2 Persons Unit
- 2 Bed / 4 Persons Unit
- 3 Bed / 6 Persons Unit
- CORRIDOR ACCESS : Ventilated stair lobby, with no flat opening directly into it
- VENTILATED LOBBY : Ventilated Lobby separating flat access from main stairwell
- VENTILATED CORRIDOR : Ventilated corridor to protect stair lobbies

0 25m

Issued For
PLANNING

General Notes:

THIS DRAWING HAS BEEN PREPARED BY MICHAEL EALES ARCHITECTS AND THE DATA CONTAINED HEREIN MAY BE USED OR REPRODUCED ONLY WITH MICHAEL EALES ARCHITECTS' APPROVAL.

Rev.	Description	Date	Signed	Checked


A3 Scale	Date	Drawn by	Checked by
1:200@A3	03.08.26	AL	ME

Drawing Title
Proposed Scheme

Project
The Grange, Bank Ln, London SW15 5JT

ME ARCHITECTS
UNIT 201 Media House,
Sopers Road, Potters Bar EN6 4RY
T - 07764 496 345
E - info@me-architects.co.uk

Project no.	Drawing no.	Revision
26/393	200	P03

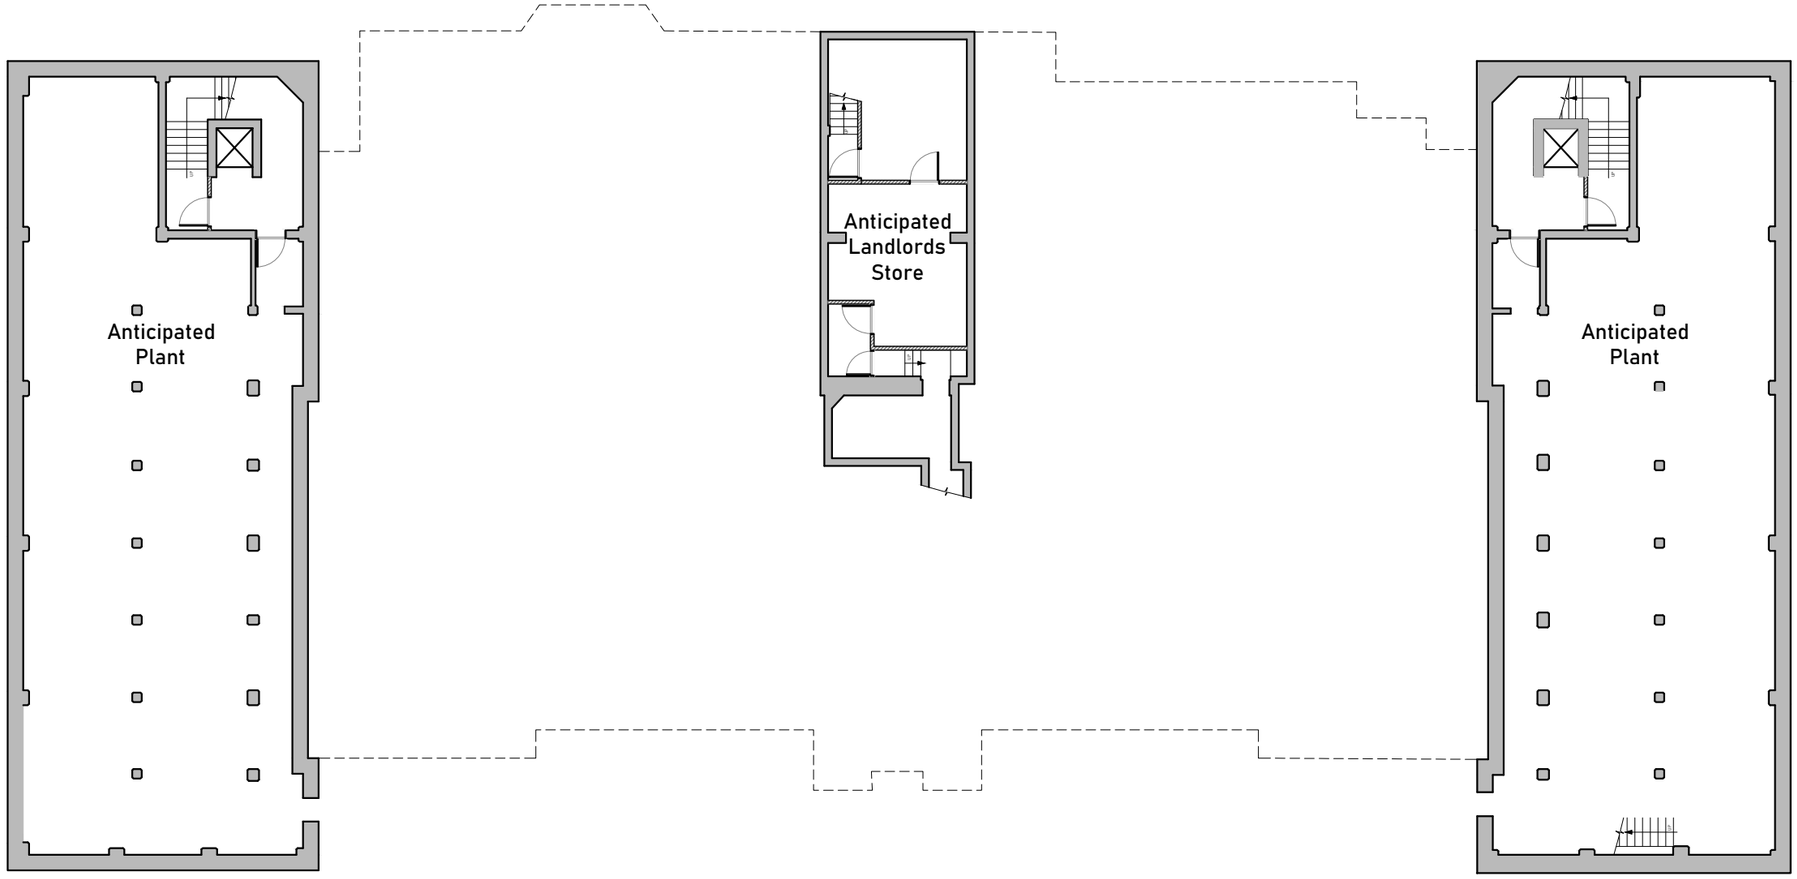

N

Proposed Basement Floor Plan

Scale 1:200 @ A3

0 10m

Issued For
PLANNING

General Notes:

THIS DRAWING HAS BEEN PREPARED BY MICHAEL EALES ARCHITECTS AND THE DATA CONTAINED HEREIN MAY BE USED OR REPRODUCED ONLY WITH MICHAEL EALES ARCHITECTS' APPROVAL.

Rev.	Description	Date	Signed	Checked


A3 Scale	Date	Drawn by	Checked by
1:200@A3	03.08.26	AL	ME

Drawing Title
Proposed Basement Floor Plan

Project
The Grange, Bank Ln, London
SW15 5JT

ME ARCHITECTS
UNIT 201 Media House,
Sopers Road, Potters Bar EN6 4RY
T - 07764 496 345
E - info@me-architects.co.uk

Project no.	Drawing no.	Revision
26/393	201	P03

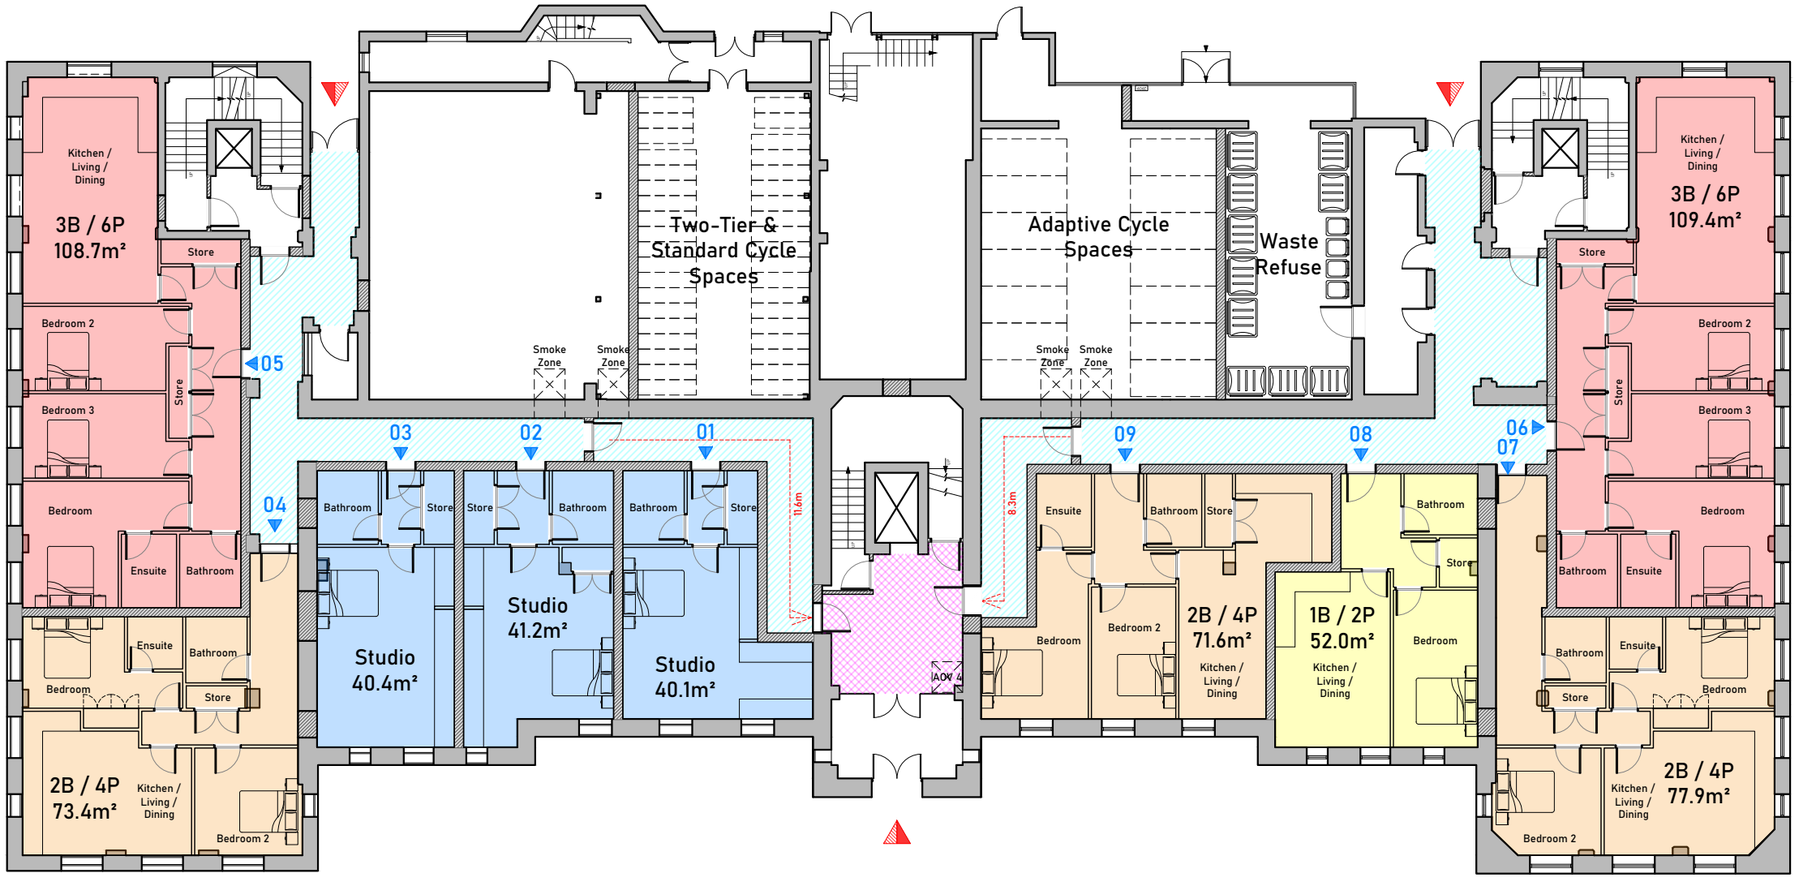

LEGEND:

- Studio Unit
- 1 Bed / 2 Persons Unit
- 2 Bed / 4 Persons Unit
- 3 Bed / 6 Persons Unit
- CORRIDOR ACCESS : Ventilated stair lobby, with no flat opening directly into it
- VENTILATED LOBBY : Ventilated Lobby separating flat access from main stairwell
- VENTILATED CORRIDOR : Ventilated corridor to protect stair lobbies

CYCLE STORE LEGEND:

- Standard Space
- Adaptive Space
- Two-Tier Space

WASTE REFUSE LEGEND:

- 240L
- 1100L
- 1260L

Proposed Ground Floor Plan

Scale 1:200 @ A3

0 10m

Issued For
PLANNING

General Notes:

THIS DRAWING HAS BEEN PREPARED BY MICHAEL EALES ARCHITECTS AND THE DATA CONTAINED HEREIN MAY BE USED OR REPRODUCED ONLY WITH MICHAEL EALES ARCHITECTS' APPROVAL.

Rev.	Description	Date	Signed	Checked


A3 Scale	Date	Drawn by	Checked by
1:200@A3	03.08.26	AL	ME

Drawing Title
Proposed Ground Floor Plan

Project
The Grange, Bank Ln, London SW15 5JT

ME ARCHITECTS
UNIT 201 Media House,
Sopers Road, Potters Bar EN6 4RY
T - 07764 496 345
E - info@me-architects.co.uk

Project no.	Drawing no.	Revision
26/393	202	P03

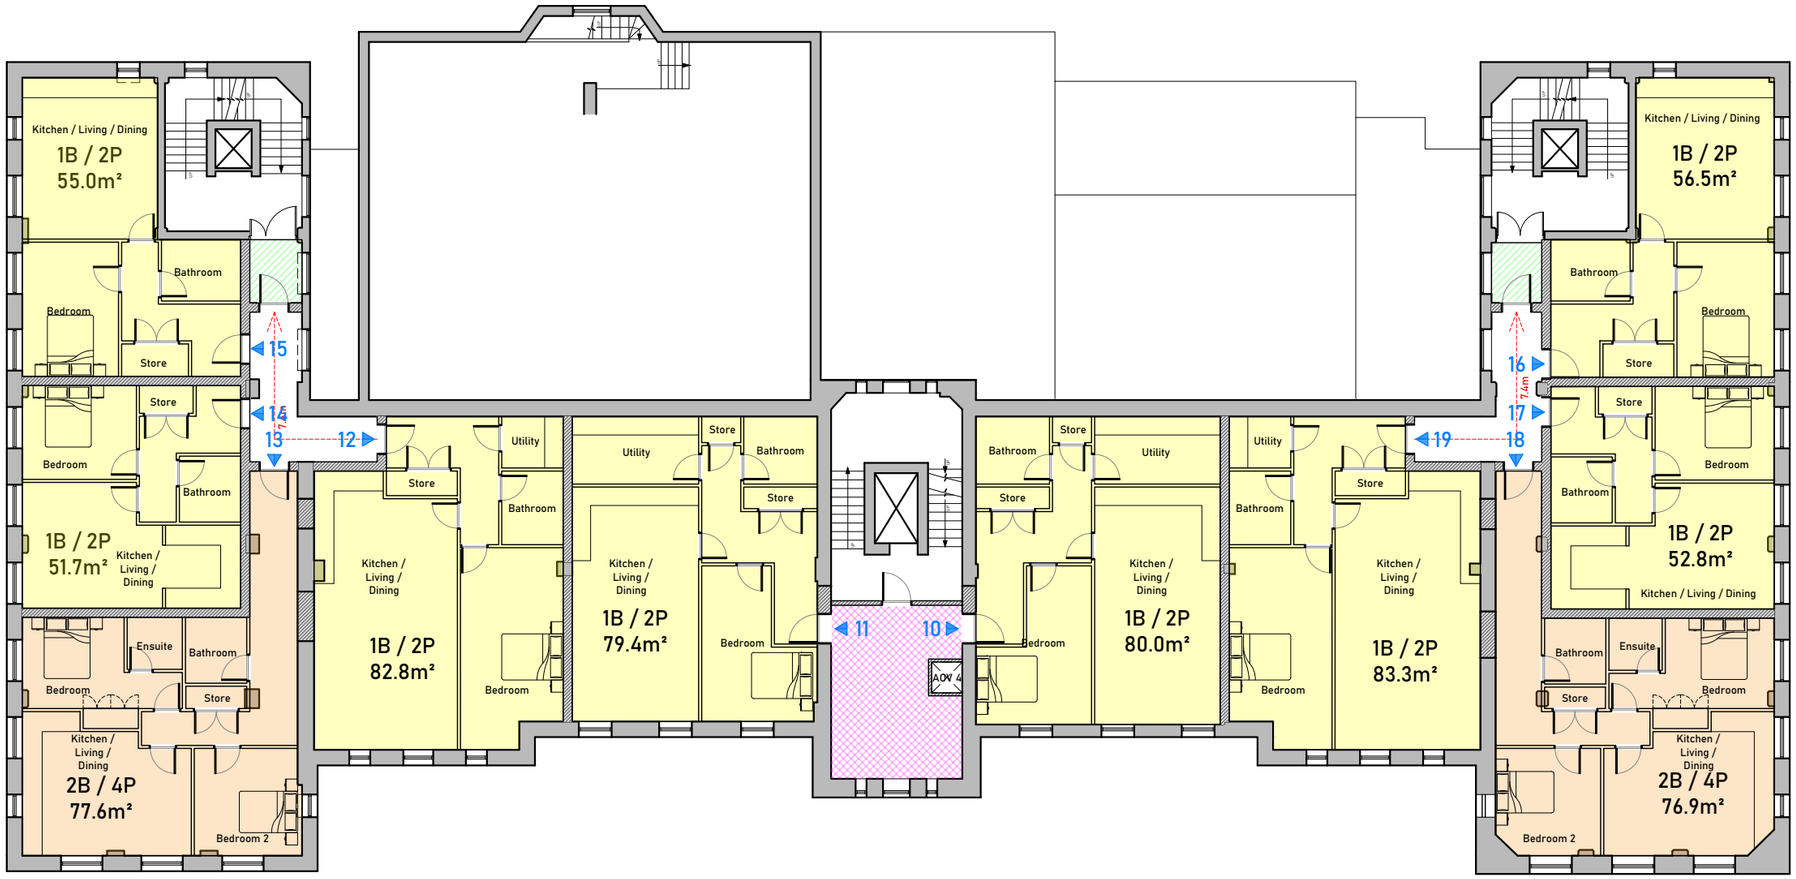

LEGEND:

- Studio Unit
- 1 Bed / 2 Persons Unit
- 2 Bed / 4 Persons Unit
- 3 Bed / 6 Persons Unit
- CORRIDOR ACCESS : Ventilated stair lobby, with no flat opening directly into it
- VENTILATED LOBBY : Ventilated Lobby separating flat access from main stairwell
- VENTILATED CORRIDOR : Ventilated corridor to protect stair lobbies

Proposed First Floor Plan

Scale 1:200 @ A3

0 10m

Issued For
PLANNING

General Notes:

THIS DRAWING HAS BEEN PREPARED BY MICHAEL EALES ARCHITECTS AND THE DATA CONTAINED HEREIN MAY BE USED OR REPRODUCED ONLY WITH MICHAEL EALES ARCHITECTS' APPROVAL.

Rev.	Description	Date	Signed	Checked


A3 Scale	Date	Drawn by	Checked by
1:200@A3	03.08.26	AL	ME

Drawing Title
Proposed First Floor Plan

Project
The Grange, Bank Ln, London SW15 5JT

ME ARCHITECTS
UNIT 201 Media House,
Sopers Road, Potters Bar EN6 4RY
T - 07764 496 345
E - info@me-architects.co.uk

Project no.	Drawing no.	Revision
26/393	203	P03

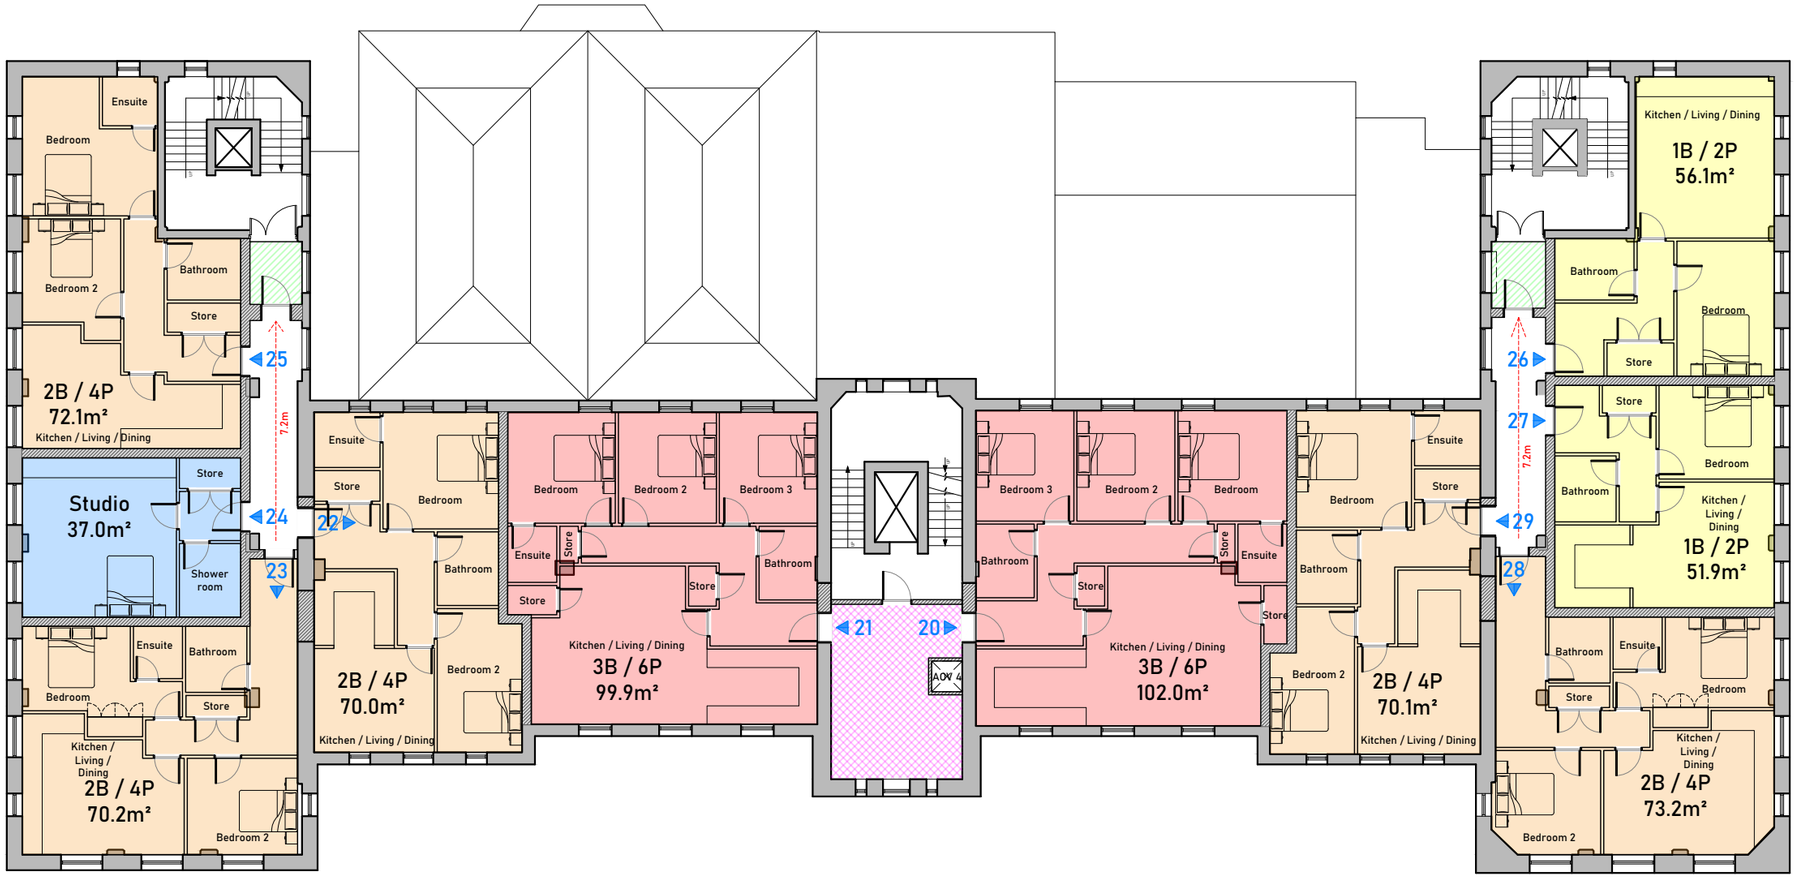

LEGEND:

- Studio Unit
- 1 Bed / 2 Persons Unit
- 2 Bed / 4 Persons Unit
- 3 Bed / 6 Persons Unit
- CORRIDOR ACCESS : Ventilated stair lobby, with no flat opening directly into it
- VENTILATED LOBBY : Ventilated Lobby separating flat access from main stairwell
- VENTILATED CORRIDOR : Ventilated corridor to protect stair lobbies

Proposed Second Floor Plan

Scale 1:200 @ A3

0 10m

Issued For
PLANNING

General Notes:

THIS DRAWING HAS BEEN PREPARED BY MICHAEL EALES ARCHITECTS AND THE DATA CONTAINED HEREIN MAY BE USED OR REPRODUCED ONLY WITH MICHAEL EALES ARCHITECTS' APPROVAL.

Rev.	Description	Date	Signed	Checked


A3 Scale	Date	Drawn by	Checked by
1:200@A3	03.08.26	AL	ME

Drawing Title
Proposed Second Floor Plan

Project
The Grange, Bank Ln, London SW15 5JT

ME ARCHITECTS
UNIT 201 Media House,
Sopers Road, Potters Bar EN6 4RY
T - 07764 496 345
E - info@me-architects.co.uk

Project no.	Drawing no.	Revision
26/393	204	P03

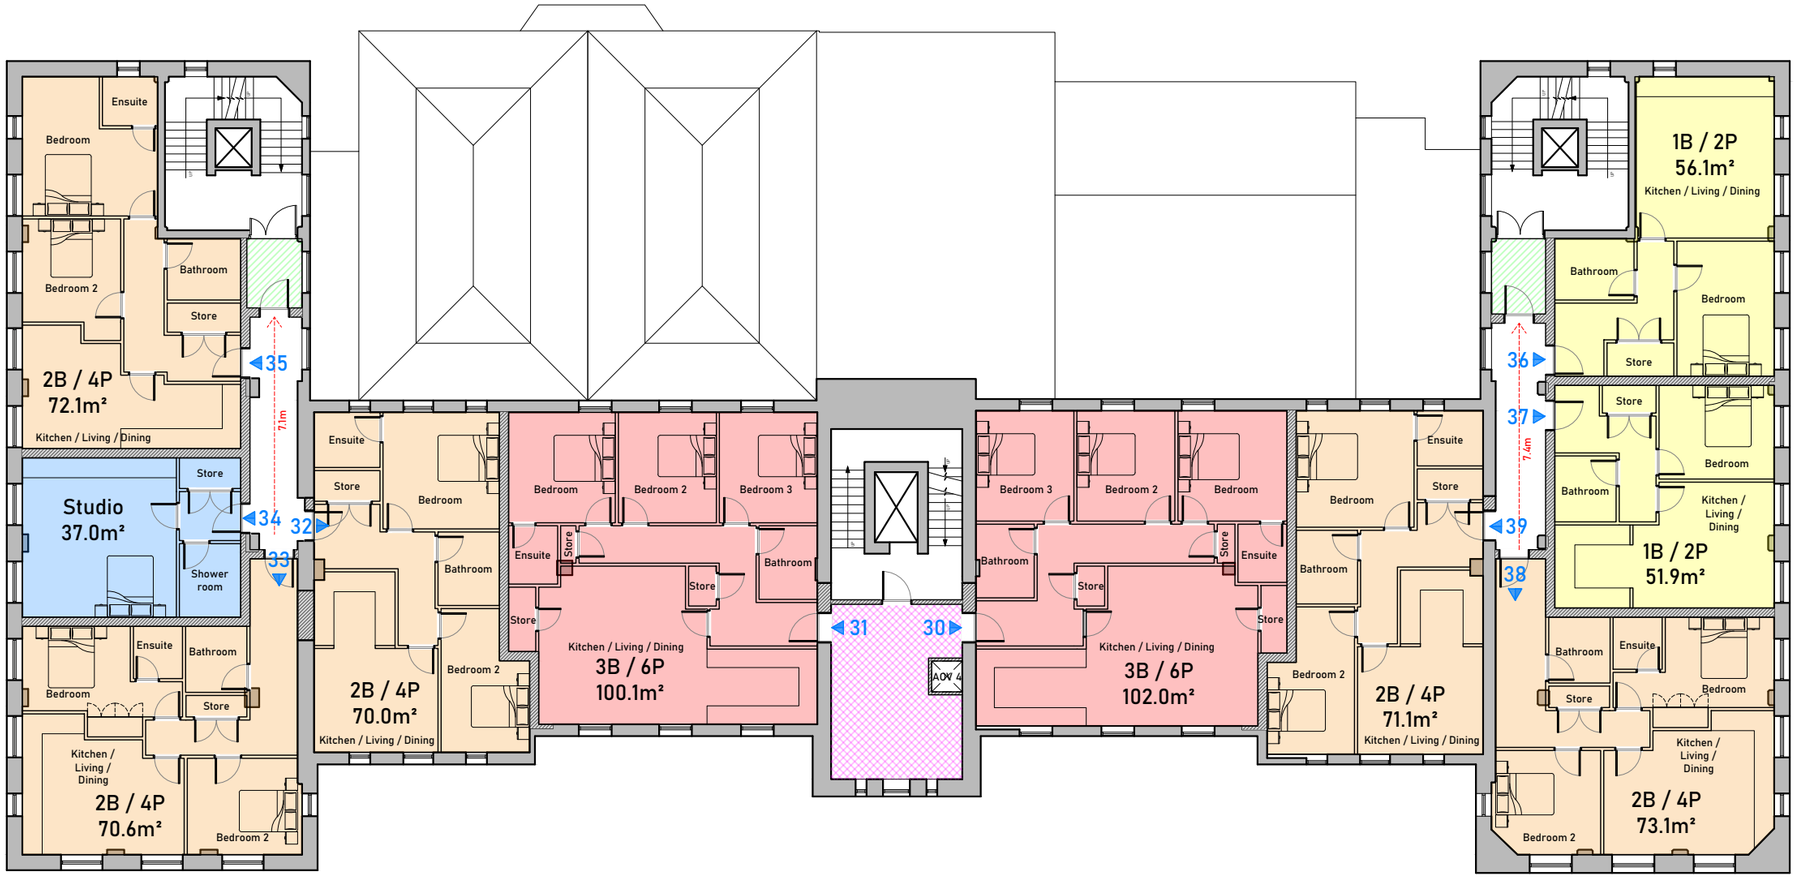

LEGEND:

- Studio Unit
- 1 Bed / 2 Persons Unit
- 2 Bed / 4 Persons Unit
- 3 Bed / 6 Persons Unit
- CORRIDOR ACCESS : Ventilated stair lobby, with no flat opening directly into it
- VENTILATED LOBBY : Ventilated Lobby separating flat access from main stairwell
- VENTILATED CORRIDOR : Ventilated corridor to protect stair lobbies

Proposed Third Floor Plan

Scale 1:200 @ A3

0 10m

Issued For
PLANNING

General Notes:

THIS DRAWING HAS BEEN PREPARED BY MICHAEL EALES ARCHITECTS AND THE DATA CONTAINED HEREIN MAY BE USED OR REPRODUCED ONLY WITH MICHAEL EALES ARCHITECTS' APPROVAL.

Rev.	Description	Date	Signed	Checked


A3 Scale	Date	Drawn by	Checked by
1:200@A3	03.08.26	AL	ME

Drawing Title
Proposed Third Floor Plan

Project
The Grange, Bank Ln, London SW15 5JT

ME ARCHITECTS
UNIT 201 Media House,
Sopers Road, Potters Bar EN6 4RY
T - 07764 496 345
E - info@me-architects.co.uk

Project no.	Drawing no.	Revision
26/393	205	P03

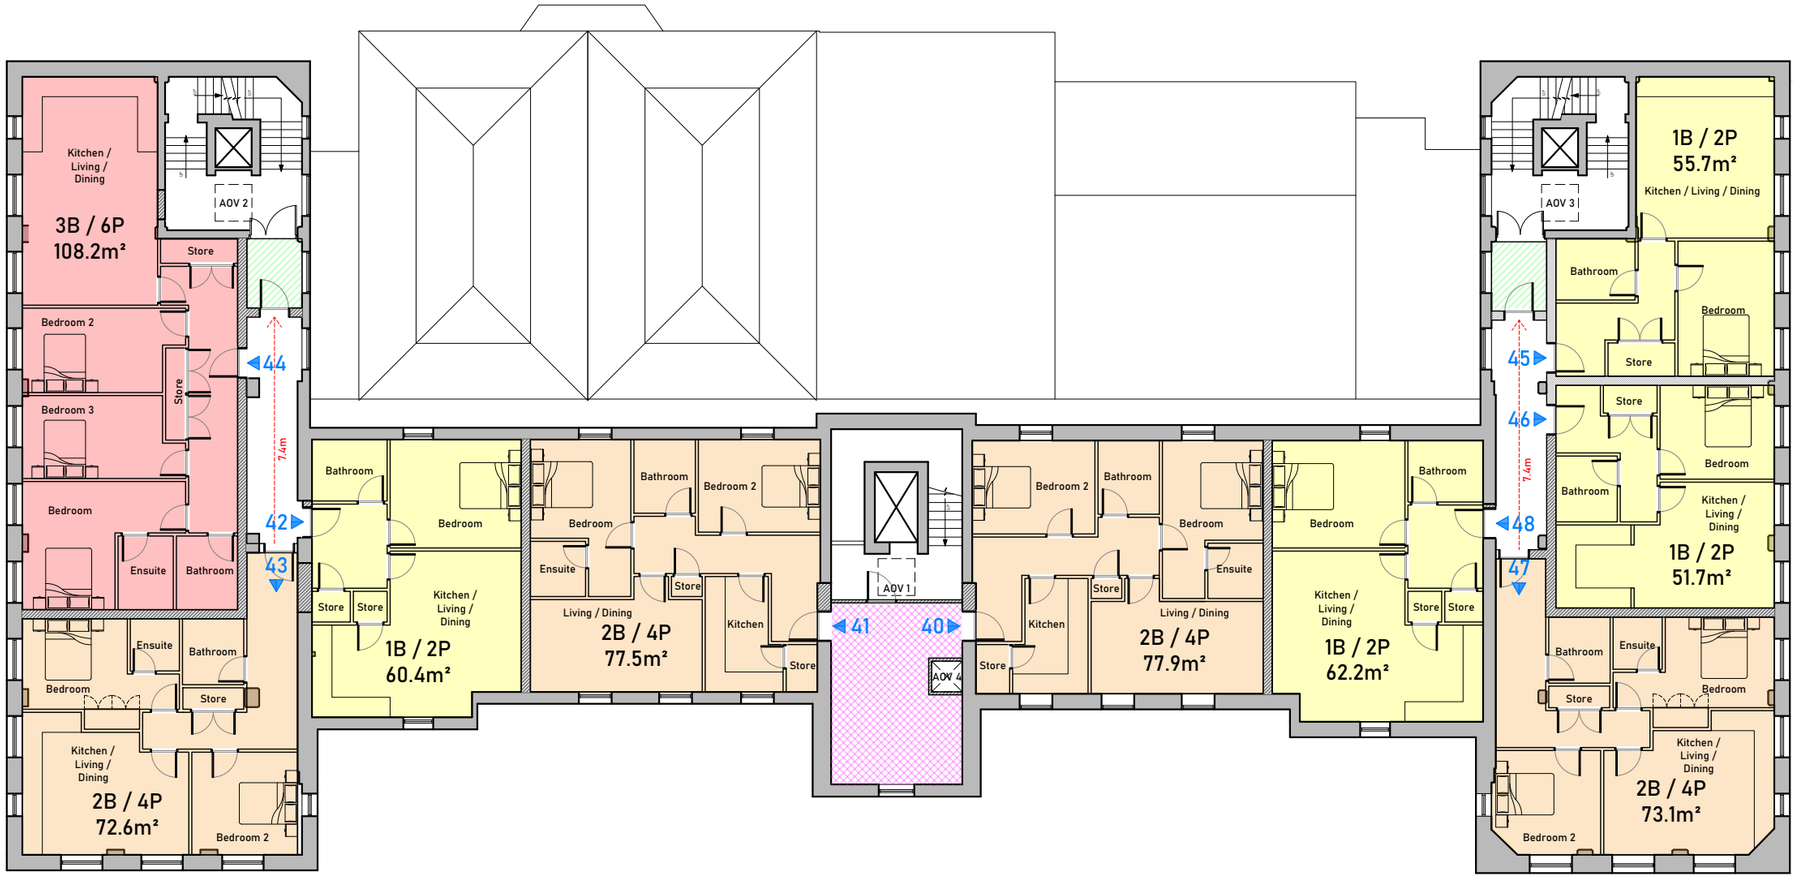

LEGEND:

- Studio Unit
- 1 Bed / 2 Persons Unit
- 2 Bed / 4 Persons Unit
- 3 Bed / 6 Persons Unit
- CORRIDOR ACCESS : Ventilated stair lobby, with no flat opening directly into it
- VENTILATED LOBBY : Ventilated Lobby separating flat access from main stairwell
- VENTILATED CORRIDOR : Ventilated corridor to protect stair lobbies

Proposed Fourth Floor Plan

Scale 1:200 @ A3

0 10m

Issued For
PLANNING

General Notes:

THIS DRAWING HAS BEEN PREPARED BY MICHAEL EALES ARCHITECTS AND THE DATA CONTAINED HEREIN MAY BE USED OR REPRODUCED ONLY WITH MICHAEL EALES ARCHITECTS' APPROVAL.

Rev.	Description	Date	Signed	Checked


A3 Scale	Date	Drawn by	Checked by
1:200@A3	03.08.26	AL	ME

Drawing Title
Proposed Fourth Floor Plan

Project
The Grange, Bank Ln, London SW15 5JT

ME ARCHITECTS
UNIT 201 Media House,
Sopers Road, Potters Bar EN6 4RY
T - 07764 496 345
E - info@me-architects.co.uk

Project no.	Drawing no.	Revision
26/393	206	P03

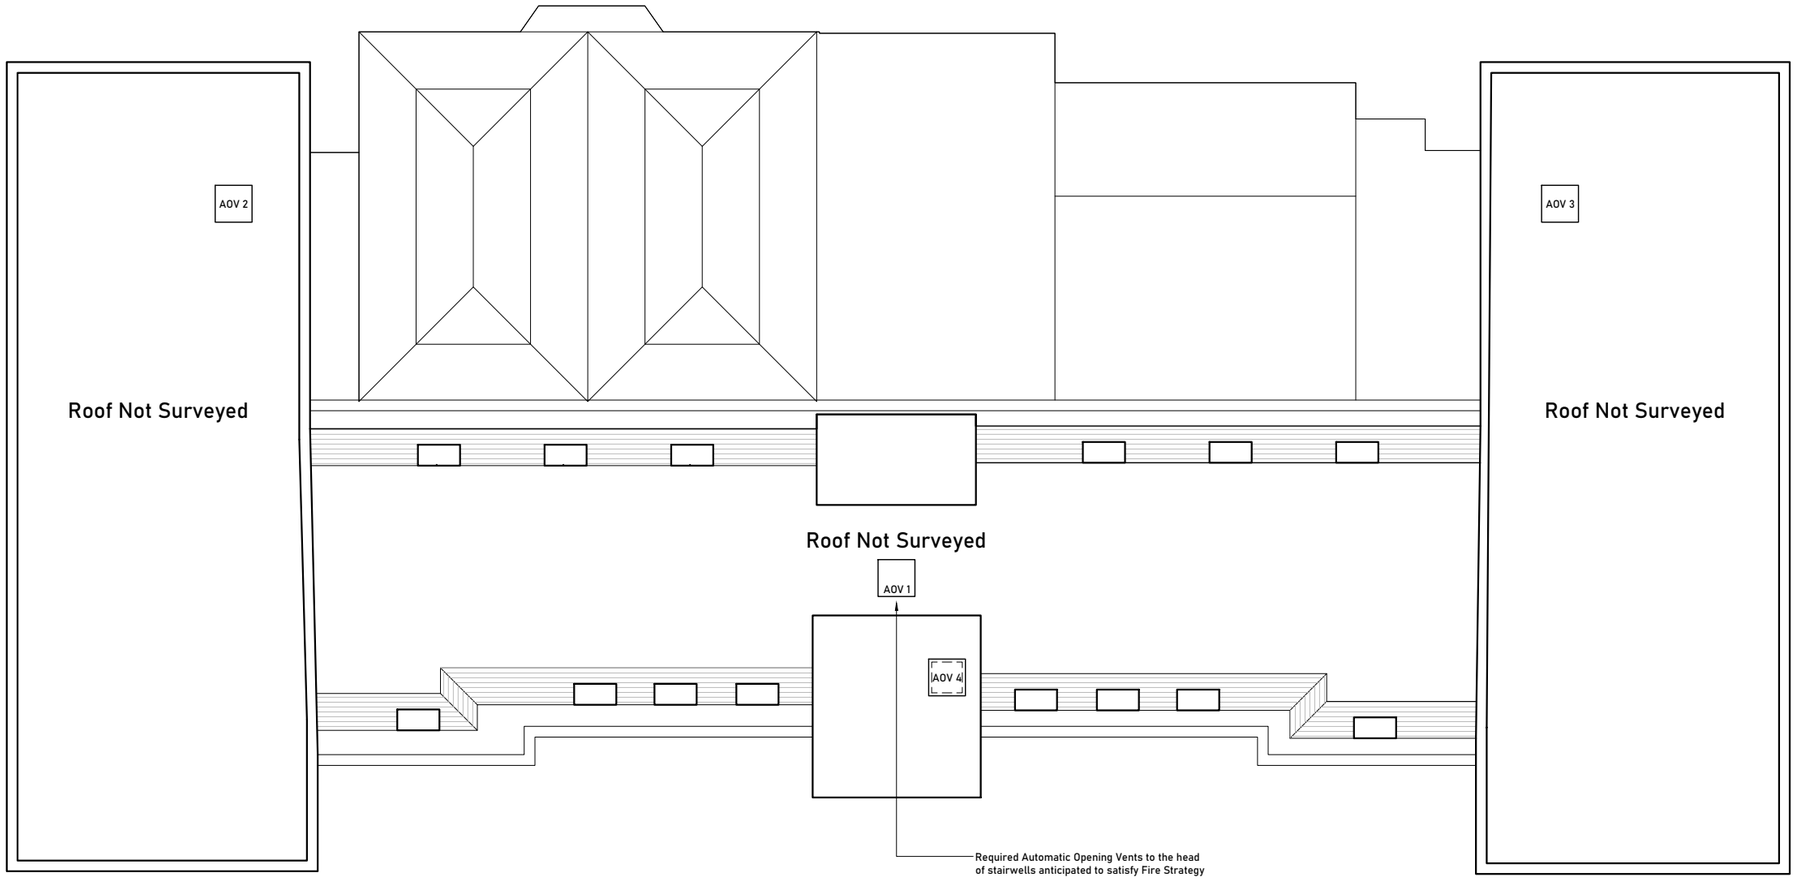

Proposed Roof Plan

Scale 1:200 @ A3

0 10m

Issued For
PLANNING

General Notes:

THIS DRAWING HAS BEEN PREPARED BY MICHAEL EALES ARCHITECTS AND THE DATA CONTAINED HEREIN MAY BE USED OR REPRODUCED ONLY WITH MICHAEL EALES ARCHITECTS' APPROVAL.

Rev.	Description	Date	Signed	Checked

A3 Scale	Date	Drawn by	Checked by
1:200@A3	03.08.26	AL	ME

Drawing Title
Proposed Roof Plan

Project
The Grange, Bank Ln, London
SW15 5JT

ME ARCHITECTS
UNIT 201 Media House,
Sopers Road, Potters Bar EN6 4RY
T - 07764 496 345
E - info@me-architects.co.uk

Project no.	Drawing no.	Revision
26/393	207	P03