
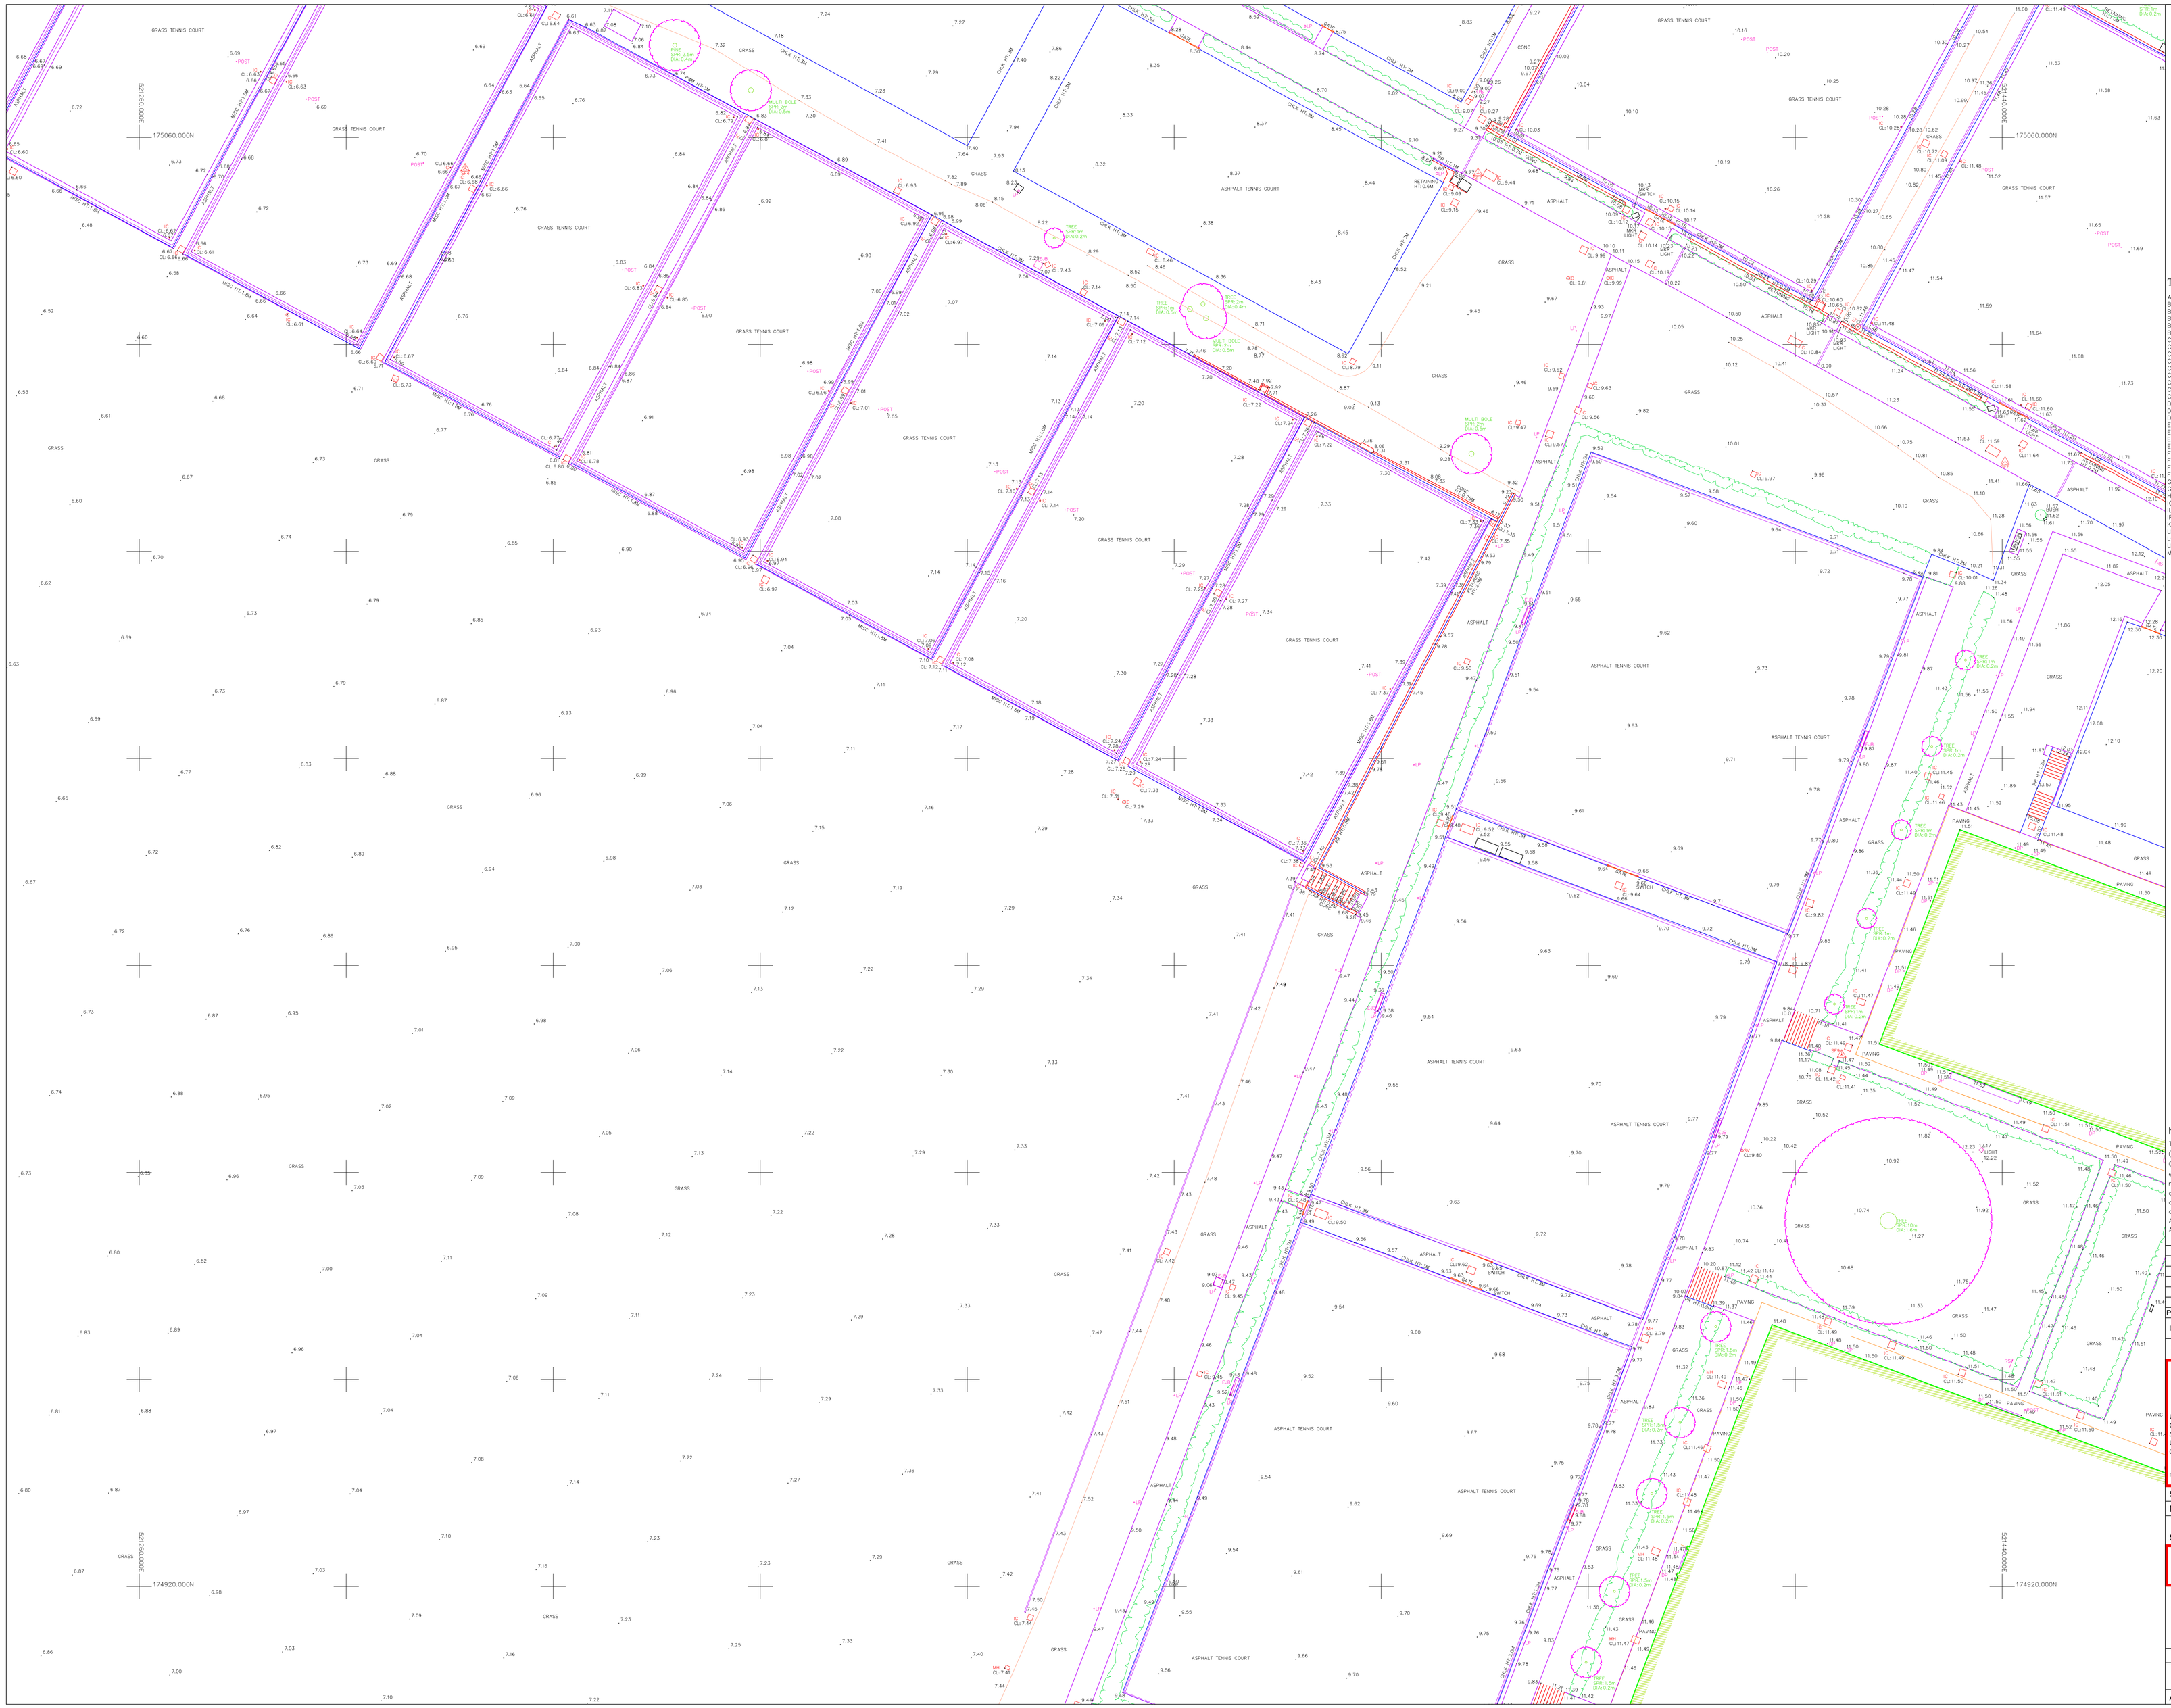


Topographical Abbreviations

A/R	Assumed Route	MKR	Marker
BH	Borehole	MT	Mercury Telecom Cover
BOL	Bollard	OHC	Overhead Cable
BT	British Telecom Cover	OHP	Overhead Pipe
BW	Barbed Wire Fence	OSBM	Ordnance Survey Bench Mark
BWK	Brickwork	PB	Post Box
CATV	Cable TV Cover	PGM	Permanent Ground Marker
CB	Close Boarded Fence	PR	Post & Rail Fence
CCTV	Closed Circuit TV	PW	Post & Wire Fence
CHLK	Chainlink Fence	PWM	Post & Wire Mesh Fence
CHPL	Chestnut Paling Fence	RE	Rodding Eye
CL	Cover Level	RG	Road Gully
CM	Cable Marker	RN	Road Name
CP	Catch Pit	RS	Road Sign
CPL	Catch Pit Base Level	RW	Retaining Wall
DIA	Diameter	RWP	Rain Water Pipe
DK	Drop Kerb	SAP	Sapling
DP	Down Pipe	SC	Stop Cock
EJB	Electricity Junction Box	SPR	Spread
EC	Electricity Cover	STA	Traverse Station
EP	Electricity Pole	SV	Stop Valve
ER	Earthing Rod	SVP	Soil Vent Pipe
FCL	Finished Ceiling Level	SW	Storm Water
FH	Fire Hydrant	TB	Telephone Box
FIG	Feed Into Ground	TBM	Temporary Bench Mark
FW	Foul Water	TFR	Taken From Records
GU	Gully	TJB	Telephone Junction Box
GV	Gas Valve	TPT	Trial Pit
H	Height	TL	Traffic Light
IC	Inspection Cover	TP	Telephone Pole
IL	Invert Level	UTL	Unable To Lift
IR	Iron Railing Fence	UTT	Unable To Trace
KO	Kerb Outlet	VP	Vent Pipe
LB	Litter Bin	WKH	Water Key Hole
LC	Lamp Column	WM	Water Meter
LP	Lamp Post	WV	Water Valve
MH	Manhole		

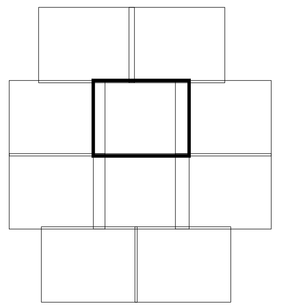

SURVEY STATIONS			
Name	Easting	Northing	Height
STN1	521262.519	174849.262	8.041
STN2	521315.276	174805.562	9.502
STN3	521296.543	174734.921	10.006
STN3A	521325.796	174732.695	10.239
STN4	521330.858	174724.919	12.010
STN5	521352.432	174775.613	12.065
STN6	521350.008	174798.840	10.161
STN7	521357.410	174828.260	9.860
STN8	521407.524	174781.629	13.079
STN9	521435.890	174798.616	14.581
STN10	521436.869	174815.469	13.589
STN10A	521375.054	174836.682	11.467
STN11	521455.372	174880.404	13.898
STN12	521480.367	174945.522	15.257
STN13	521525.037	174949.608	15.851
STN14	521550.191	174939.276	16.584
MS1	521379.495	174709.811	14.856
MS2	521445.277	174644.985	17.117
MS3	521466.199	174703.187	16.998
MS4	521492.208	174754.395	17.952
MS5	521497.177	174803.850	16.048
MS6	521531.670	174861.464	16.339
N1	521369.629	174844.930	9.903
N2	521379.399	174880.147	9.530
N3	521389.511	174882.670	11.688
SF1	521186.539	174899.218	6.595
SF2	521163.026	175008.041	6.112
SF3	521193.121	175090.245	6.623
SF4	521291.491	175256.992	6.683
SF5	521316.578	175096.307	7.103
SF6	521440.285	175028.670	11.629
SF7	521389.355	175056.556	9.396
SF8	521537.665	174988.646	15.324
SF9	521424.488	174971.359	11.481

Notes

The survey has been oriented to Ordnance Survey (OS) National Grid (OSGB36) using Industry Standard Network RTK GPS equipment utilising the OS Active Network (OS Net). A true OSGB36 coordinate has been established on site using the OSTN15 (transformation) & OSGB15 (geoid) models. The survey detail has been correlated to this point and a further one (or more) OSGB36 points established to produce a true OS bearing for angle orientation. Scale factor 1.0 has been applied therefore the survey coordinates are shown on a pseudo OS grid.
All levels are in metres unless otherwise specified
All heights are in millimetres unless otherwise specified

Rev	Svyr	QA Check	Description	Date
5	-	-	-	-
4	-	-	-	-
3	-	-	-	-
2	-	-	-	-
1	-	-	-	-
0		AH	First Complete Issue	27/08/2019
Prelim		-	Preliminary - Not Complete	-

© Copyright Warner Surveys

Drawn in BricsCAD – www.bricsys.com part of www.hexagon.com

WARNER SURVEYS
Land and Engineering Surveying Since 1979

Unit 22, Theale Lakes Bus. Pk, Moulden Way READING. RG7 4GB T +44 (0)118 930 3314
G 3 Bedford House, 69-79 Fulham High St LONDON. SW6 3JW T +44 (0)203 651 7540
5th Floor 1 Temple Way BRISTOL. BS2 0BY T +44 (0)117 301 8137
Unit G9, The Arch, 48-52 Floodgate St BIRMINGHAM. B5 5SL T +44(0)121 752 1220
Queens Court, 9-17 Eastern Road ROMFORD. RM1 3NH T +44(0)121 752 1220

www.warnersurveys.com contact@warnersurveys.com
Topographic, Utility, Measured Building & LiMV Surveys Movement, Deformation & Environmental Monitoring
Construction, Site Engineering & 3D Laser Scanning Oil, Gas & Industrial Surveying & Dimensional Control

SURVEYED	WS	Gerald Eve
DRAWN	WS	
SCALE	1:200	

Bank of England Sports Centre

TOPOGRAPHICAL SURVEY

JOB No	DRAWING NUMBER
RT/319/0418	RT/319/0418/P/0004

A0 Sheet - 1,189mm X 841mm