

Front (West) Elevation

Scale 1:200 @ A3

0 10m

Issued For
PLANNING

General Notes:

THIS DRAWING HAS BEEN PREPARED BY MICHAEL EALES ARCHITECTS AND THE DATA CONTAINED HEREIN MAY BE USED OR REPRODUCED ONLY WITH MICHAEL EALES ARCHITECTS' APPROVAL.

Rev.	Description	Date	Signed	Checked


A3 Scale	Date	Drawn by	Checked by
1:200@A3	03.09.26	PS	ME

Drawing Title
Proposed Elevations


Project
The Grange, Bank Lane, SW15 5JT

ME ARCHITECTS
UNIT 201 Media House,
Sopers Road, Potters Bar EN6 4RY
T - 07764 496 345
E - info@me-architects.co.uk

Project no.	Drawing no.	Revision
26/393	210	00

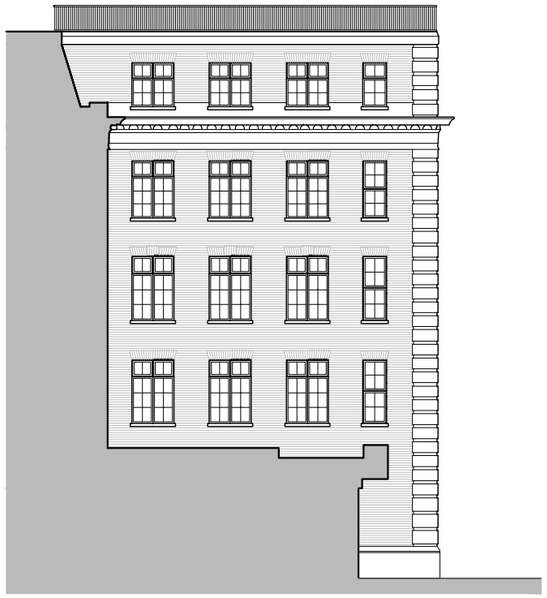

Rear Projection (South) Elevation
Scale 1:200 @ A3

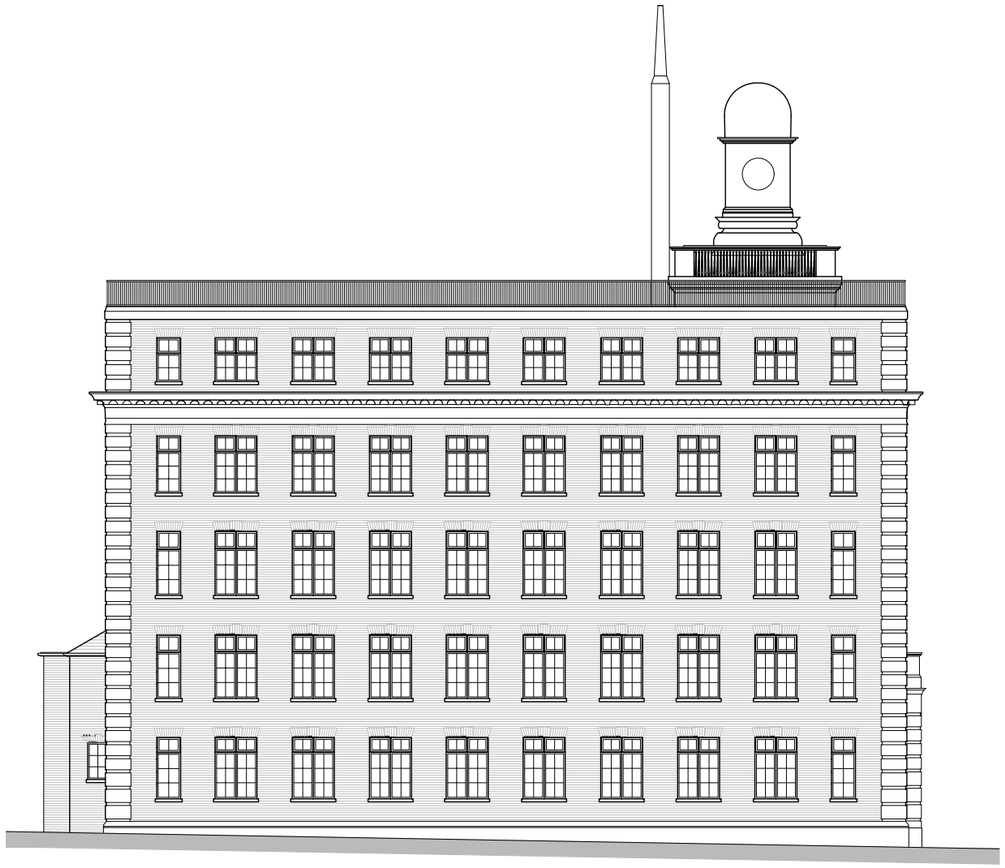

Side (North) Elevation
Scale 1:200 @ A3

0 10m

Issued For
PLANNING

General Notes:

THIS DRAWING HAS BEEN PREPARED BY MICHAEL EALES ARCHITECTS AND THE DATA CONTAINED HEREIN MAY BE USED OR REPRODUCED ONLY WITH MICHAEL EALES ARCHITECTS' APPROVAL.

Rev.	Description	Date	Signed	Checked

A3 Scale	Date	Drawn by	Checked by
1:200@A3	03.09.26	PS	ME

Drawing Title
Proposed Elevations

Project
The Grange, Bank Lane, SW15 5JT

ME ARCHITECTS
UNIT 201 Media House,
Sopers Road, Potters Bar EN6 4RY
T - 07764 496 345
E - info@me-architects.co.uk

Project no.	Drawing no.	Revision
26/393	211	00



Rear (East) Elevation

Scale 1:200 @ A3

0 10m

Issued For
PLANNING

General Notes:

THIS DRAWING HAS BEEN PREPARED BY MICHAEL EALES ARCHITECTS AND THE DATA CONTAINED HEREIN MAY BE USED OR REPRODUCED ONLY WITH MICHAEL EALES ARCHITECTS' APPROVAL.

Rev.	Description	Date	Signed	Checked


A3 Scale	Date	Drawn by	Checked by
1:200@A3	03.09.26	PS	ME

Drawing Title
Proposed Elevations


Project
The Grange, Bank Lane, SW15 5JT

ME ARCHITECTS
UNIT 201 Media House,
Sopers Road, Potters Bar EN6 4RY
T - 07764 496 345
E - info@me-architects.co.uk

Project no.	Drawing no.	Revision
26/393	212	00

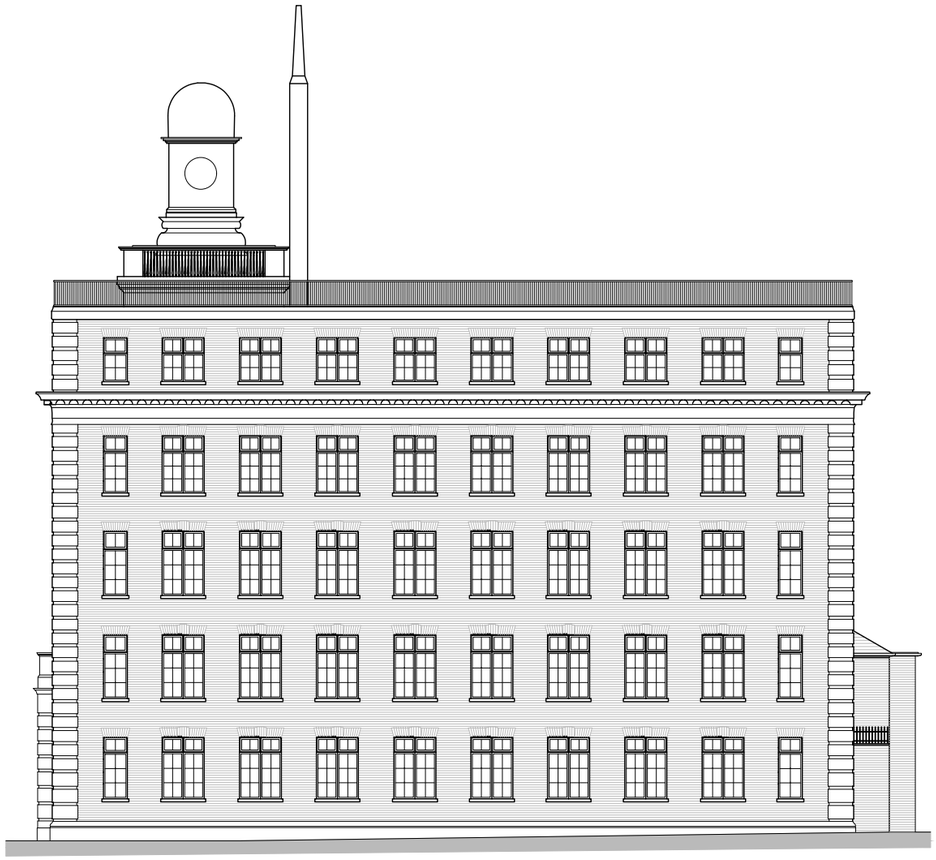

Side (South) Elevation
Scale 1:200 @ A3

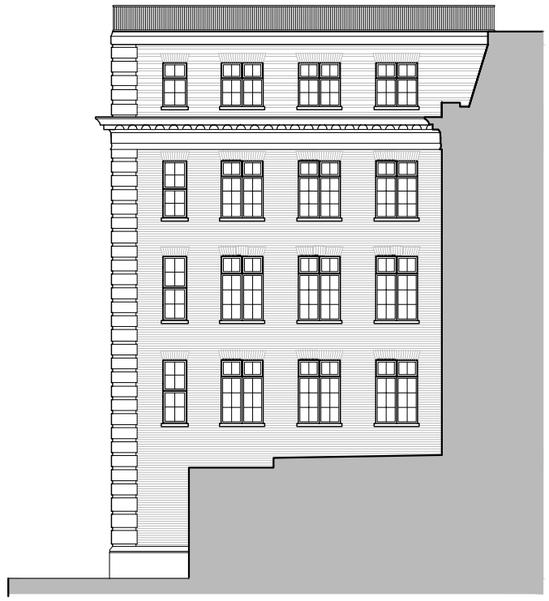

Rear Projection (North) Elevation
Scale 1:200 @ A3

0 10m

Issued For
PLANNING

General Notes:

THIS DRAWING HAS BEEN PREPARED BY MICHAEL EALES ARCHITECTS AND THE DATA CONTAINED HEREIN MAY BE USED OR REPRODUCED ONLY WITH MICHAEL EALES ARCHITECTS' APPROVAL.

Rev.	Description	Date	Signed	Checked

A3 Scale	Date	Drawn by	Checked by
1:200@A3	03.09.26	PS	ME

Drawing Title
Proposed Elevations

Project
The Grange, Bank Lane, SW15 5JT

ME ARCHITECTS
UNIT 201 Media House,
Sopers Road, Potters Bar EN6 4RY
T - 07764 496 345
E - info@me-architects.co.uk

Project no.	Drawing no.	Revision
26/393	213	00